


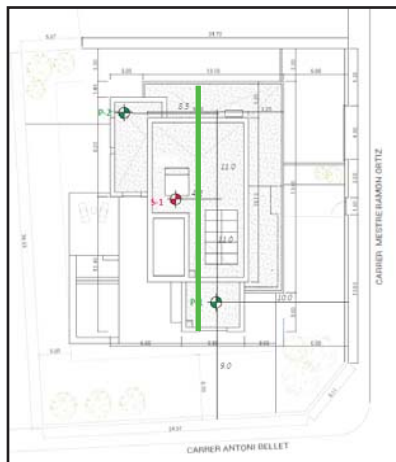

# LLEGENDA




Sòls vegetals



1er nivell: Graves amb sorres



Cota de fonamentació

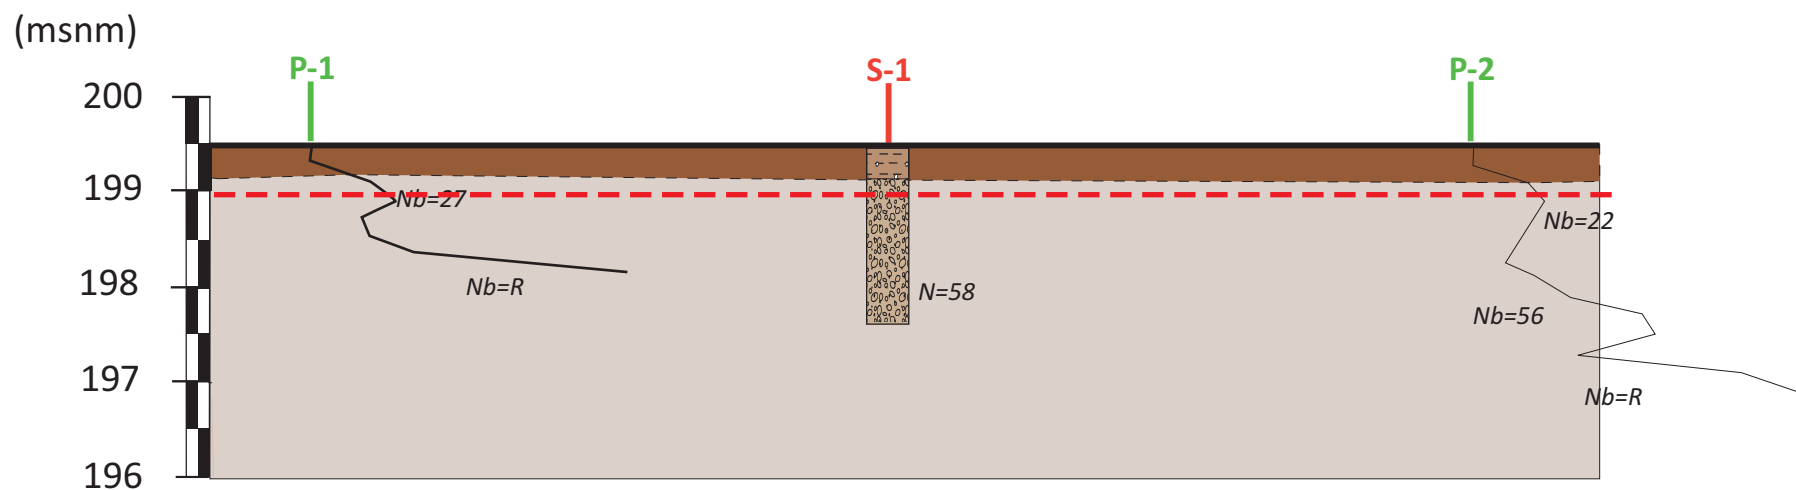

## TÍTOL DEL PROJECTE

ESTUDI GEOLÒGIC I GEOTÈCNIC PER LA CONSTRUCCIÓ D'UN HABITATGE UNIFAMILIAR AÏLLAT  
SITUAT ENTRE EL CARRER ANTONI BELLET I CARRER MESTRE RAMON ORTIZ DE BELL-LLOC

Data: Octubre 2025

Exp: 4001612

Plànol de situació

Pàgina 1/1