

CLIENT:

EXPEDIENT: 3001621

DATA: 21/11/25

OBRA: Estudi geològic / geotècnic per la CONSTRUCCIÓ D'UN
GRUP D'HABITATGES UNIFAMILIARS AL CARRER ARBRELLS
18A, 18B i 20 a CASTELLAR DEL VALLÈS





Índex

1 . PRESENTACIÓ DE L'ESTUDI	3
1.1. ANTECEDENTS.....	3
1.2. CLASSIFICACIÓ DE L'OBRA SEGONS EL CTE.....	4
1.3. OBJECTIUS.....	4
2. TREBALLS DE CAMP	5
2.1. DESCRIPCIÓ DE LA ZONA D'ESTUDI.....	5
2.1.1. <i>Descripció de les parcel·les adjacents</i>	5
2.1.2. <i>Descripció del solar</i>	5
2.2. RECONeixEMENT DEL TERRENY.....	6
2.3. JUSTIFICACIÓ DE COMPLIMENT DE CTE.....	7
2.4. DESCRIPCIÓ DELS ASSAIGS IN SITU.....	7
2.4.1. <i>Assaigs de penetració tipus "DPSH"</i>	7
2.4.2. <i>Sondeig a Rotació amb Bateria Contínua</i>	8
2.4.3. <i>Assaig tipus S.P.T. ("Standard Penetration Test")</i>	9
2.4.4. <i>Resum dels assaigs in-situ realitzats</i>	10
2.5. ASSAIGS DE LABORATORI.....	11
3. DESCRIPCIÓ GEOLÒGICA I GEOTÈCNICA.....	12
3.1. MARC GEOLÒGIC.....	12
3.2. CARACTERITZACIÓ DELS MATERIALS	14
3.2.1. <i>1er nivell</i>	14
3.3. HIDROLOGIA I HIDROGEOLOGIA.....	15
3.3.1. <i>Hidrogeologia superficial</i>	15
3.3.2. <i>Hidrogeologia subterrània</i>	15
3.3.3. <i>Permeabilitat dels materials</i>	15
3.4. AGRESSIVITAT DEL MEDI.....	16
3.5. EXCAVABILITAT.....	16
3.6. ACCELERACIÓ SISMICA DE REFERÈNCIA	17
3.7. EXPOSICIÓ AL GAS RADÓ	18
4. CONCLUSIONS.....	20
4.1. GEOLOGIA	20
4.2. HIDROGEOLOGIA I AGRESSIVITAT	21
4.3. FONAMENTACIÓ	21
4.4. EMPENTES DE TERRES	22
4.5. ESTABILITAT DEL VESSANT	22



Annexes

Base de càlcul

Registre assaigs mecànics

Esquema situació assaigs

Tall de correlació

Fotografies

Actes d'assaig de laboratori

1 . PRESENTACIÓ DE L'ESTUDI

A petició de:

G3 DT, S.L. ha realitzat el següent informe geotècnic segons les instruccions del DB SE-C Cimientos fetes pel “Código Técnico de la Edificación” CTE, que entrà en vigor el 29 de març del 2006.

1.1. ANTECEDENTS

Segons ens indica el sol·licitant, -----es vol valorar les característiques geològiques i geotècniques dels materials del subsòl on es preveu construir 3 habitatges unifamiliars d'estructura lleugera, fusta.

L'edificació que es preveu construir presentarà les següents característiques:

Nº de plantes per habitatge	Pb+1Pp
Superfície de la parcel·la (m²)	1.284
Superfície construïda total (m²)	120 m²

Taula 1. Resum de les principals dades de l'edificació a construir.

El solar on s'emplaçarà els nous habitatges unifamiliars e situa en el Carrer dels Arbrells, 18A,18B i 20 de Castellar del Vallès.

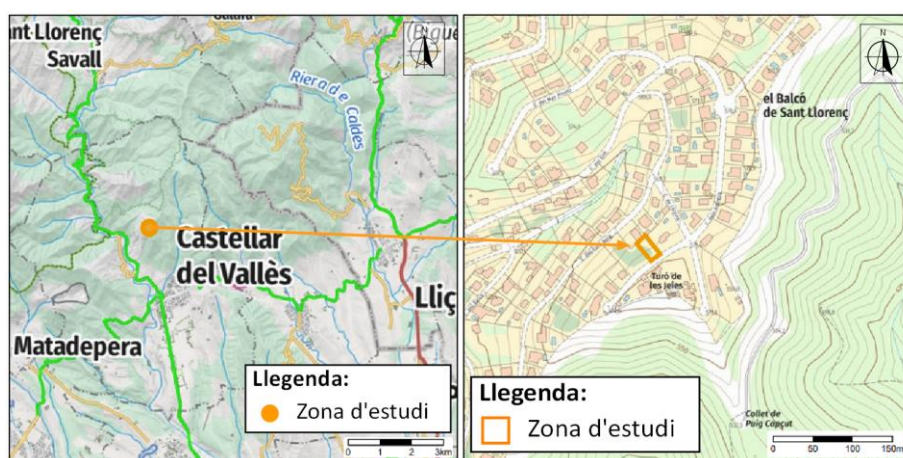


Figura 1. Situació de la zona d'estudi, amb color taronja. (mapes topogràfic i ortofoto, ICGC 2025, modificat).

1.2. CLASSIFICACIÓ DE L'OBRA SEGONS EL CTE

A partir de les dades exposades pel client, tant tipus d'edificació com localització de l'obra, un tècnic qualificat en la realització de l'estudi realitza la següent classificació, segons els criteris que marca el DB SE-C del citat CTE:

Tipus d'edificació considerada:	C-1
Tipus de sòl considerat :	T-1

Taula 2. Classificació de la construcció segons DB-SE-C del CTE.

1.3. OBJECTIUS

Per la realització del present estudi, s'ha dut a terme una campanya de camp tenint en compte que els objectius de l'estudi són:

- Estudi de l'entorn geològic de l'obra.
- Reconeixement, caracterització i potència dels materials del subsòl de la zona, des del punt de vista geològic i geotècnic, i tenint en compte les recomanacions del CTE.
- Cota del nivell freàtic, quan es detecti dins de les cotes assajades.
- Determinació de les càrregues admissibles dels materials sota diferents solucions de fonamentació.
- Estimació dels assentaments per a les càrregues admissibles exposades.
- Recomanacions sobre condicionants geològics i geotècnics que puguin afectar a l'obra.



2. TREBALLS DE CAMP

El dia 24 de octubre de 2025, es va visitar l'obra per tal de:

- Realitzar una inspecció geològica de la zona, reconeixent el tipus de terreny.
- Dissenyar la campanya de camp.
- Comprovar l'accessibilitat de maquinària a l'interior del solar.
- Localitzar els punts on es realitzaran els assaigs.

2.1. DESCRIPCIÓ DE LA ZONA D'ESTUDI

2.1.1. Descripció de les parcel·les adjacents

La parcel·la objecte d'estudi es situa al nord del municipi de Castellar del Vallès, pren una morfologia quasi rectangular, i limita:

- Per la part nord, amb parcel·les sense construir, amb herbes altes i arbres, així com una parcel·la amb planta baixa i una planta pis, paral·lela al carrer Turó Roig.
- Per la part sud, amb el carrer Arbrells.
- Per la part est, amb una parcel·la construïda amb piscina.
- I finalment, per la part oest, amb parcel·les sense construir amb herbes altes i arbres.

2.1.2. Descripció del solar

El dia dels treballs de camp es realitza l'entrada a la zona d'estudi a través del carrer adjacent situat al sud.

El solar es localitza sense construccions ni pavimentacions, s'ha realitzat un desbroç de la zona de treball i s'ha adequat un accés a la zona de treball.

Topogràficament, el solar presenta pendent, amb una plataforma de treball, la única on es pot emplaçar la màquina, situada aproximadament 4.0 metres respecte el carrer.

En solars propers existeixen construccions de característiques similars a la obra projectada que el dia dels treballs de camp no presentaven patologies aparents a les seves parets exteriors visibles.

Destacar que no es poden veure aflorar els materials del subsòl del solar ni en la parcel·la objecte d'estudi ni en zones properes.

2.2. RECONeixEMENT DEL TERRENY

La campanya de camp, que s'ha realitzat el dia 24 de octubre de 2025, ha consistit en la realització de:

- 4 assaigs de penetració dinàmica tipus DPSH (veure annex "Registre assaigs mecànics").
- 1 sondeig a rotació amb bateria continua (veure annex "Registre assaigs mecànics").
- 1 assaig SPT amb recuperació de mostra (veure annex "Registre assaigs mecànics").
- Observacions de camp realitzades pel tècnic de l'empresa desplaçat a l'obra.
- Reportatge fotogràfic (veure annex "Fotografies").

Els assaigs in situ han estat realitzats per TPS PROSPECCIÓ DEL SUBSÒL, S.L., laboratori d'assaigs per al control de qualitat de l'edificació.



Figura 2. Emplaçament de l'habitatge projecte i els assaigs realitzats.

2.3. JUSTIFICACIÓ DE COMPLIMENT DE CTE

A partir de la campanya realitzada i la classificació de l'obra que s'obté segons l'apartat 1.2 del present estudi, es compleixen els mínims establerts pel DB SE-C del Código Técnico de la Edificación pel que fa referència al nombre de punts d'investigació realitzats, així com a les profunditats assolides en els mateixos i distància mínima entre ells.

2.4. DESCRIPCIÓ DELS ASSAIGS IN SITU

2.4.1. Assaigs de penetració tipus “DPSH”

L'assaig consisteix a clavar en el terreny una barnilla de secció circular mitjançant la caiguda d'una massa, per penetrar en intervals de 20 cm l'esmentada barilla. El comptatge del número de cops ens donarà un valor que anomenarem N_{20} , amb el que podrem obtenir la resistència a la penetració dinàmica del terreny en punta (ja que la punta és d'un diàmetre superior que la barnilla i no es produeix resistència per fuste), així com la compacitat del terreny granular.

En el cas que el nombre de cops necessaris per travessar els 20 cm, sigui superior a 100, o quan es superin 3 intervals consecutius de 75 cops considerarem rebuig a la penetració i s'abandonarà l'assaig.

Característiques de l'assaig:

Alçada de caiguda del Pes: 75 cm

Diàmetre de la punta de penetració: 51 mm

Interval de penetració: 20 cm

Pes : 63.5 Kg

En aquest cas s'utilitza la màquina de penetració **ML-76A**.




Fotografia 1. Vista de la màquina utilitzada en un dels assaigs de penetració dinàmica realitzats.

2.4.2. Sondeig a Rotació amb Bateria Contínua

Els sondejos a rotació amb bateria contínua són perforacions de petit diàmetre que permeten reconèixer la naturalesa i la localització de les diferents capes del terreny, així com extreure mostres del mateix i realitzar assaigs *in situ*.

Els sondejos amb bateria contínua consisteixen en la perforació mitjançant un mecanisme de rotació equipat d'una bateria, normalment d' 1.5m. Aquesta bateria s'introdueix en el terreny per un mètode de rotació, i un cop plena es treu i es recupera la mostra recollida durant l'avanç del sondatge.

Aquest tipus d'assaigs s'utilitzen en roques o en sòls durs, i els diàmetres habituals són entre 66 i 143mm. En aquest cas s'utilitza la mateixa màquina de penetració ML-76A, equipada amb un capçal a rotació.

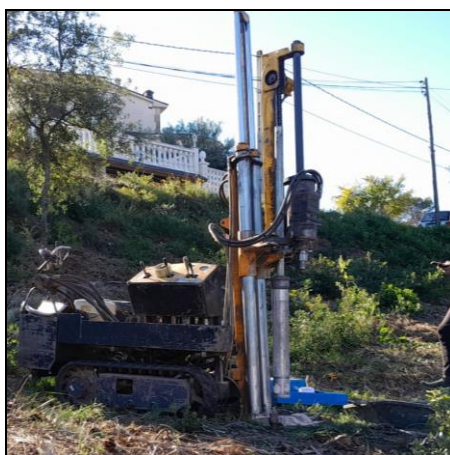

Fotografia 2. Vista de la màquina utilitzada per a la realització del sondeig a rotació.

2.4.3. Assaig tipus S.P.T. ("Standard Penetration Test")

Per realitzar aquest assaig s'ha d'avançar primer amb un assaig normal fins arribar a la cota on interessa realitzar el test. En aquest punt s'introdueix la *cullera normalitzada** fins el fons i es colpeja amb la massa. No es conten els cops necessaris per introduir els primers 15 centímetres, ja que se suposa que el terreny en el fons del sondeig pot estar alterat. Si que es conten els cops realitzats per introduir la cullera els següents 45 centímetres en trams de 15. La suma dels colpeigs dels dos trams centrals és el "**número de penetració estàndard**", N_{SPT} o N_{30} . En el cas que el darrer dels trams tingui un valor de colpeig menor que el dels dos trams centrals, se sumaran els dos valors més petits dels tres darrers trams enregistrats.

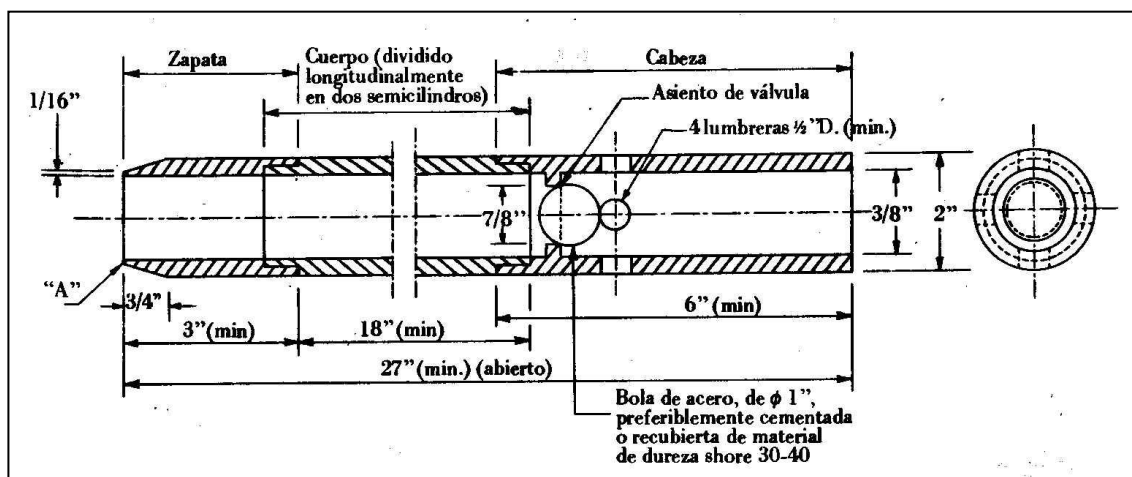


Figura 3. Cullera normalitzada. Gràfic extret de "Geotècnia y cimientos II" (J.A. Jiménez Salas, J.L. de Justo Alpañés, A.A. Serrano González).

Dins la cullera es recupera la mostra. Aquesta mostra es considera remoldejada ja que el gruix de les parets del tub és molt gran en relació al diàmetre interior. De tota manera, permet conèixer la composició granulomètrica dels materials

2.4.4. Resum dels assaigs in-situ realitzats

Els assaigs de camp realitzats es sintetitzen en el quadre que s'exposa a continuació:

Penetròmetres dinàmics DPSH				
Punt	Cota d'inici (m*)	Profunditat assolida (m)	Rebuig	Humitat (m)
P-1	-4.0	-1.08	Si	No detectat
P-2	-4.20	-0.48	Si	No detectat
P-3	-4.0	-0.76	Si	No detectat
P-4	-4.0	-1.55	Si	No detectat

Sondeig a rotació bateria continua				
Punt	Cota d'inici (msnm*)	Profunditat assolida (m)	SPT/MA	Humitat (m)
S-1	-4.20	-1.20	1/0	No detectat

Assaigs SPT / MA				
Nº assaig	Punt	Prof. Extracció (m)	N ₃₀	Litologia
SPT-1	S-1	-1.00 a -1.20	R	Limolites i bretxes

Taula 3, 4 i 5. Resum dels assaigs in situ realitzat. *msnm: metres sobre el nivell del mar.

Les cotes d'inici estan referenciades respecte la superfície actual del solar respecte el carrer Arbrells, per on es realitza l'entrada al solar. Aquesta cota pot variar lleugerament donat que no es realitza un replantejament dels punts en el solar.



2.5. ASSAIGS DE LABORATORI

Els assaigs de laboratori han estat realitzats per TPS PROSPECCIÓ DEL SUBSÒL SL (SOIL ASSAIG), laboratori d'assaigs per al control de qualitat de l'edificació.

Donada la naturalesa dels materials s'han sol·licitat els següents assaigs:

<i>Mostra : SPT-1</i>	<i>Punt: S-1</i>	<i>Profunditat: -1.00 a -1.20 m</i>
<i>Assaigs realitzats</i>	<i>1 assaig de contingut en sulfats UNE 83963 : 2008</i>	

Taula 6. Resum dels assaigs de laboratori realitzats.

3. DESCRIPCIÓ GEOLÒGICA I GEOTÈCNICA

3.1. MARC GEOLÒGIC

En primer lloc s'ha procedit a la consulta de les diferents cartografies geològiques existents sobre la zona:

- Full 13: Barcelonès, del Mapa geològic comarcal de Catalunya, 1:50000 de l'ICC, 2005.
- Hoja 392: Sabadell, del Mapa geológico de España, 1:50000 de l'IGME, 1975.

El present estudi s'emmarca gairebé al mig de la Depressió del Vallès-Penedès, la qual es disposa en una orientació NNE a SSO. Es tracta d'una fossa tectònica, que separa les serralades Litoral i Prelitoral corresponents a la Cadena Costanera Catalana.

La depressió es va formar a inicis del Miocè, dins d'una etapa de "rifting" relacionada amb la creació d'una conca marina entre Catalunya i Balears, dins el context de la Mediterrània Occidental, quan es va produir l'enfonsament del materials paleozoics i mesozoics de l'antic Massís Catalano-Balear. Aquests materials enfonsats es van convertir en el sòcol sobre el qual es va dipositar la potent sèrie miocena, que reomple l'esmentada depressió.

Pel que respecta a les serralades que flanquegen la depressió, la Prelitoral està formada per:

- Quarsites i pissarres cambro-ordovicianes.
- Granodiorites i granits alcalins que van intruir durant el Carbonífer i el Permian.
- Per damunt apareix la sèrie Triàsica, la qual comença amb els gresos i lutites coneguts com Fàcies Buntsandstein, del Triàsic inferior. Continua amb les Fàcies Muschelkalk, representades per dos potents nivells de calcàries i dolomies separats per un altre nivell de gresos i argiles. Aquest segon conjunt comprèn des del Triàsic mitjà al superior.
- Finalment, la sèrie culmina amb la potent successió de materials conglomerats i gresos de l'Eocè que formen els relleus de la zona de Montserrat.

La Serralada Litoral per la seva part, està formada gairebé únicament en aquesta zona quarsites i pissarres cambroordovicianes del Paleozoic.

Pel que fa a la Depressió del Vallès-Penedès, la sèrie estratigràfica miocena està representada per:

- Lutites vermelles i grises i guixos, durant el Burdigalià superior, que representen dipòsits de transició continental-marí.
- Argiles fossilíferes i llims del Burdigalià-Serraval·lià.
- A continuació afloren els conglomerats, argiles i sorres arcòsiques de l'Aragonià-Vallesià. Aquests són possiblement els materials més representats a la zona del Vallès.
- Per damunt continuen les argiles blaves, gresos i sorres argiloses del Serraval·lià-Tortonià, amb menor representació.
- Els conglomerats amb matriu sorrenca del Miocè superior afloren sobretot a la zona de Terrassa.

Fora ja de la sèrie miocena, es dipositen les successions de materials quaternaris, els quals estan representats per:

- Dipòsits associats als ventalls al·luvials procedents de la Serralada Prelitoral i que desembocaven a l'interior de la depressió. Edat Pleistocè.
- Dipòsits de terrasses fluvials i dipòsits al·luvials originats pels cursos fluvials actuals, que drenen la depressió en sentit N-S Edat Pleistocè-Holocè.

En concret, i segons l'ICGC, l'estudi s'ha dut a terme damunt una zona on afloren materials de la unitat **ECbc**, corresponent a *bretxes amb intercalacions de lutites i gresos vermells del Eocè- l'presià*.

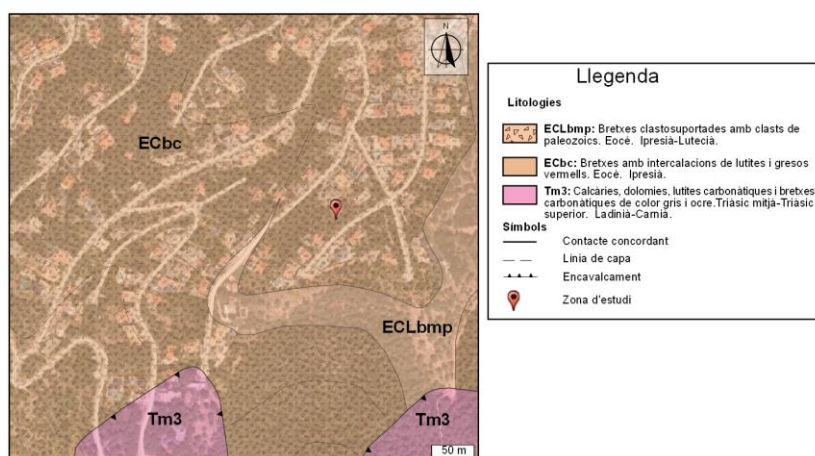


Figura 4. Mapa geològic a escala 1:25.000 de la zona en estudi (ICGC, modificat).

3.2. CARACTERITZACIÓ DELS MATERIALS

A partir dels assaigs in situ realitzats, s'ha establert **un sòl nivel de materials** des del punt de vista geològic - geotècnic: (veure annex “Registre assaigs mecànics”):

1er nivell *Bretxes amb intercalacions de lutites i gresos vermells.
Substrat rocós.*

Per damunt d'aquests materials es detecta un tram superficial format per Llims argilosos color marró fosc amb graves i algunes arrels. Terreny Vegetal. Amb potències entre 0.4 i 0.80 metres.

3.2.1. 1er nivell

Descripció litològica

El **1er nivell** està format per **bretxes amb intercalacions de lutites i gresos vermells**.



Fotografia 4. Detall dels materials recuperats durant la realització del sondeig S-1.

Aquests materials han estat caracteritzats a partir de la interpretació de les dades dels assaigs mecànics, i a partir de la correlació amb la geologia regional de la zona.

Aquest nivell s'ha identificat com materials d'edat Eocè, unitat ECbc segons l'ICGC, mapa 1:25.000.

Localització

Aquests materials es detecten per sota dels materials del primer nivell descrit i fins a la cota de finalització dels assaigs, amb una potència màxima detectada de **1.15 m** amb els assaigs realitzats, tot i que a partir de l'estudi de la geologia regional de la zona se li associa potències molt superiors.

Resistència

Des del punt de vista geomecànic es tracta d'uns materials amb un **comportament des de friccional a roca dura, amb una densitat i una capacitat portant de mitja a elevada**. Dels assaigs de penetració dinàmica s'obté valors de Nb des de 44 a ràpidament rebuig a la penetració en profunditat, Nb>100.

3.3. HIDROLOGIA I HIDROGEOLOGIA

3.3.1. Hidrogeologia superficial

Tot i no ser un solar pla, no s'han detectat marques i/o indicis de processos d'erosió relacionats amb l'escolament hídric superficial, ni es preveu que apareguin.

Tampoc s'ha localitzat cap curs d'aigua i/o torrent proper que pugui afectar a la zona en estudi. Amb tot, donada la pendent de la zona, es recomana dimensionar una correcta xarxa de recollida d'aigües per a què no circuli lliurement damunt de la superfície del solar.

3.3.2. Hidrogeologia subterrània

En data de la realització dels treballs de camp, i fins la cota assajada, no es va detectar presència de nivell freàtic en cap dels assaigs realitzats.

3.3.3. Permeabilitat dels materials

A continuació s'exposen els valors del coeficient de permeabilitat (K) associats als materials detectats al subsòl del solar:

Nivell	K (m/s)	Tipus material
1er nivell	$10^{-5} - 10^{-7}$	Bretxes amb intercalacions de lutites i gresos vermells.

Taula 7. Resum del coeficient de permeabilitat dels materials del subsòl.

3.4. AGRESSIVITAT DEL MEDI

D'una mostra dels materials del subsòl, on es preveu armar la fonamentació, s'ha realitzat els pertinents assaigs de laboratori per tal de determinar la seva agressivitat al formigó (segons CE-21).

Els resultats obtinguts s'exposen en la següent taula:

Nivell	Contingut en sulfats (mg/kg SO ₄)	Acidesa Baumann-Gully (ml/kg)	Qualificació (*)
1er nivell	0.0	--	No Agressius

Taula 8. Valors obtinguts dels assaigs de laboratori.

(1) Segons el Real decreto 470/2021, de 29 de junio, publicat al B.O.E. amb data 10/08/21.

(*) Per a classificar el grau d'agressivitat dels materials front al formigó segons la taula de classificació de l'agressivitat química de el Código Estructural 21 (Real decreto 470/2021, de 29 de junio, publicat al B.O.E. amb data 10/08/21), a més a més del contingut en sulfats es deurà realitzar un assaig d'acidesa de Baumann-Gully, tot i que en aquest cas, i degut a les característiques dels materials no es considera necessària realitzar aquest assaigs ja que no es tracta d'un valor restrictiu.

3.5. EXCAVABILITAT

Segons el projecte executiu es preveu la construcció d'estructures sense nivell de soterrani, i per tant, únicament es preveu el sanejament, anivellació, i l'excavació fins a la cota de fonamentació.

L'excavació dels trams superficials dels materials del nivell 1 es realitzarà fàcilment amb un retroexcavadora convencional. En canvi, en profunditat, en els materials del primer nivell sanejat, el rendiment de la màquina podria disminuir, essent possiblement necessària la utilització de maquinaria més contundent tipus "martell pneumàtic".

3.6. ACCELERACIÓ SÍSMICA DE REFERÈNCIA

A efectes d'aplicació de la Norma de Construcció Sismoresistente NCSE-02, es donaran el paràmetres de l'acceleració sísmica bàsica corresponent a la zona estudiada, i el coeficient C, depenent a les característiques geotècniques del terreny on es realitzarà la fonamentació.

L'acceleració sísmica s'obté del Mapa de Perillositat Sísmica inclòs en la esmentada Norma i que estableix per a cada punt del territori l'acceleració sísmica bàsica, A_B .

A la zona d'estudi, en el municipi de Castellar del Vallès, s'estableix una acceleració sísmica bàsica de:

$$A_B = 0,04 \text{ g (essent g el valor de la gravetat)}$$

L'acceleració sísmica de càlcul, A_C es defineix com el producte següent:

$$A_C = S * A_B * \rho$$

On

A_B és l'acceleració sísmica bàsica

ρ és un coeficient adimensional de risc on el seu valor es dona en funció de la vida de l'edifici en anys per la que es projecta l'edifici.

Aquest paràmetre bé donat per:

Construccions d'importància normal $\rho = 1,0$

Construccions d'importància especial $\rho = 1,3$

S coeficient d'amplificació del terreny. Es pren el valor:

$$\text{Per } \rho * A_B < 0,1g \quad S = C/1,25$$

$$\text{Per } 0,1g < \rho * A_B < 0,4g \quad S = C/1,25 + 0,33(\rho * A_B/g - 0,1)(1 - C/1,25)$$

$$\text{Per } 0,4g < \rho * A_B \quad S = 1,0$$

C: Coeficient del terreny. Aquest coeficient depèn de les característiques geotècniques del terreny on es realitza la fonamentació.

Per obtenir el coeficient C de càlcul es determinaran els espessors de cada un dels tipus de terrenys, existents els 30 primers metres sota la superfície, i s'adoptarà el valor de la mitjana ponderada.

A cada un dels nivells establerts se'ls associa el següent tipus de terreny i el següents coeficients, que queden recollits en la següent taula:

Nivells	Tipus de terreny	Gruix (metres)	Coeficient C
1	Tipus II	1.15*	1.3

Taula 9. Valors de la potencia i coeficient C pel càlcul de l'acceleració sísmica.

*Al nivell se li associa una potència superior.

El projectista o en el seu cas el promotor haurà d'establir l'ús de l'edifici al llarg de la seva vida útil, a fi d'establir la classificació dins el grup corresponent, d'acord amb el que s'estableix a la “Norma de Construcción Sismoresistente NCSE-02”.

3.7. EXPOSICIÓ AL GAS RADÓ

En el *DB Secció HS-6 Protección frente a la exposición al radón del CTE (RD 732/2019)* es determina que es necessari limitar el risc previsible d'exposició dels usuaris a concentracions inadequades de radó en edificis tancats situats en els termes municipals inclosos a l'apèndix B del document.

Aquesta secció s'aplica:

- En edificis de nova construcció
- En intervencions en edificis existents com en ampliacions, un canvi d'ús ja sigui característic de l'edifici o d'alguna zona del mateix
- En obres de reforma quan es realitzen modificacions que permetin augmentar la protecció front el radó o alterin la protecció inicial.

En l'apèndix inclou un llistat de termes municipals als que, en base a les mesures realitzades pel Consejo de Seguridad Nuclear, es considera que existeix una probabilitat significativa de que els edificis construïts a la zona sense solucions específiques de protecció en front al radó presenten concentracions de radó superiors al nivell de referència.

Per a limitar el risc d'exposició dels usuaris a concentracions inadequades de radó procedent del terreny a l'interior dels locals habitables, s'estableix un nivell de referència per a la mitjana anual de concentració de radó a l'interior dels mateixos de 300Bq/m³.

Les solucions que es poden dur a terme segons la localització del terme municipal en ZONA 1 o en ZONA 2 són:



En obra nova

- En termes municipals ZONA 1:
 - Barrera de protecció
 - Càmera d'aire ventilada
- En termes municipal ZONA 2:
 - Barrera de protecció juntament amb una càmera d'aire ventilada
 - Barrera de protecció juntament amb despressurització del terreny

Rehabilitació d'edificis

- A part de les solucions anteriors, de manera alternativa o complementaria es pot utilitzar un segellat de tancaments en contacte amb el terreny i la millora de la ventilació.

Es pot consultar la informació completa al DB Secció HS-6 Protección frente a la exposición al radón del CTE.

La parcel·la concreta d'estudi es localitza al terme municipal de CASTELLAR DEL VALLÈS i, segons la taula existent a l'apèndix B del RD 732/2019, pertany a la ZONA 1.

4. CONCLUSIONS

Les recomanacions es donen en funció dels resultats obtinguts de la campanya de camp realitzada, així com les observacions realitzades pel tècnic de l'empresa desplaçat a l'obra.

4.1. GEOLOGIA

Es detecta **un sòl nivell de materials des del punt de vista geològic/geotècnic** en el subsòl del solar en estudi.

Per damunt d'aquests materials es detecta un tram superficial format per Llims argilosos color marró fosc amb graves i algunes arrels. Terreny Vegetal. Amb potències entre 0.4 i 0.80 metres.

El **1er nivell** està format per bretxes amb intercalacions de lutites i gresos vermells. Aquest nivell s'ha identificat com materials d'edat Eocè, unitat ECbc segons l'ICGC, mapa 1:25.000. Aquests materials es detecten per sota dels materials del primer nivell descrit i fins a la cota de finalització dels assaigs, amb una potència màxima detectada de 1.15 m amb els assaigs realitzats, tot i que a partir de l'estudi de la geologia regional de la zona se li associa potències molt superiors. Des del punt de vista geomecànic es tracta d'uns materials amb un comportament des de friccional a roca dura, amb una densitat i una capacitat portant de mitja a elevada.

La distribució espacial dels materials al llarg de les parcel·les estudiades es recull en següent tall de correlació:

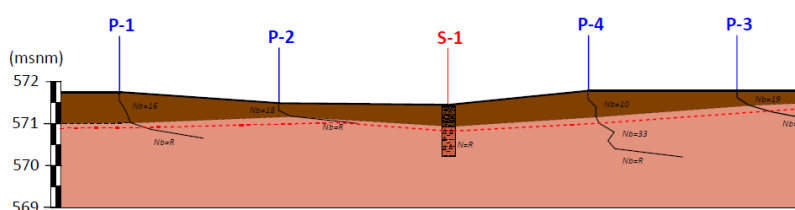


Figura 5. Tall de correlació.

Finalment, a partir de les litologies observades, s'ha associat al nivell descrit unes característiques geològiques i geotècniques que queden resumides en el quadre següent:

<i>Nivell</i>	<i>Nb</i>	<i>N</i>	<i>Densitat⁽¹⁾</i>	<i>Cohesió⁽²⁾</i>	<i>Angle de fregament intern⁽³⁾</i>	<i>E⁽⁴⁾</i>
1er nivell: Bretxes amb intercalacions de lutites i gresos	17-R	R	2.20	1.0	35°	>500

Taula 10. Característiques geològiques i geotècnics dels materials del subsol.

Els paràmetres de cohesió i angle de fregament intern, s'han obtingut de les relacions que s'estableixen en el llibre “Mecànica de suelos y cimentaciones” de l'autor Carlos Crespo Villalaz, a partir de la resistència dels materials.

⁽¹⁾Densitat està donada en gr/cm³.

^(2 i 3)La cohesió està expressada en Kg/cm². Tan la cohesió com l'angle de fregament intern són valors efectius o llarg termini.

⁽⁴⁾Mòdul de deformació, Kg/cm²

4.2. HIDROGEOLOGIA I AGRESSIVITAT

Tot i no ser un solar pla, no s'han detectat marques i/o indicis de processos d'erosió relacionats amb l'escolament hídic superficial, ni es preveu que apareguin. Tampoc s'ha localitzat cap curs d'aigua i/o torrent proper que pugui afectar a la zona en estudi.

Tampoc s'ha localitzat cap curs d'aigua i/o torrent proper que pugui afectar a la zona en estudi. Amb tot, donada la pendent de la zona, es recomana dimensionar una correcta xarxa de recollida d'aigües per a què no circuli lliurament damunt de la superfície del solar.

A partir dels resultats dels assaigs de laboratori realitzats, els materials del subsòl on es preveu armar la fonamentació, a priori, es presenten No Agressius al formigó.

4.3. FONAMENTACIÓ

Segons el projecte executiu es preveu la construcció de tres habitatges unifamiliars sense nivell de soterrani, i per tant, únicament es preveu el sanejament, anivellació, i l'excavació fins a la cota de fonamentació.

Un cop realitzada l'excavació afloraran superficialment els materials del primer nivell descrit.

Per tant, a partir de les propietats geomecàniques dels materials del primer nivell es realitzarà una valoració de ***fonamentació superficial mitjançant sabates, ja sigui aïllades i/o corregudes, i/o llosa.***

Per una **fonamentació superficial mitjançant sabates, ja sigui aïllades com corregudes, encastada entre 20-30 cm en els materials de substrat, un cop superats els materials superficials**, es podrà adoptar una **tensió de treball** de:

$$Q_a = 3.0 \text{ Kg/cm}^2 \text{ amb un factor de seguretat inclòs de } F=3$$

Els **assentaments** màxims previstos per la càrrega recomanada anteriorment seran **menyspreables o bé inferiors a 1.0 cm.**

Si s'optés per una fonamentació amb llosa, el valor de **coeficient de balast**, referit a la placa de 30x30, es podrà adoptar un valor de **$K_{30}=8.00 \text{ kg/cm}^3$** .

4.4. EMPENTES DE TERRES

Pel dimensionament del murs que es projectin i pel càlcul de les empentes de terres caldrà tenir en compte els paràmetres geomecànics dels materials del 1er nivell que es considera el més desfavorables.

Cal tenir en compte que en el trasdors del mur, caldrà instal·lar un correcte drenatge per a evitar que s'acumuli aigua i es produeixi un sobrecàrrega en el seu trasdors.

4.5. ESTABILITAT DEL VESSANT

Per a la realització de les recomanacions d'estabilitat de talussos s'han tingut en compte les següents premisses:

- Actualment el solar presenta un pendent d'entre 20-25°.
- Talussos sense presència de nivell freàtic.
- Factor de seguretat $F=1.8$, factor de seguretat del vessant actual.
- S'ha considerat la columna de materials, dominat pel primer nivell, amb els paràmetres geomecànics obtinguts.

El mètode ràpid de càlcul utilitzat per les recomanacions de talussos és el proposat per Hoek & Bray (1977), utilitzant els valors numèrics de cohesió, angle de fregament i densitat exposat anteriors.

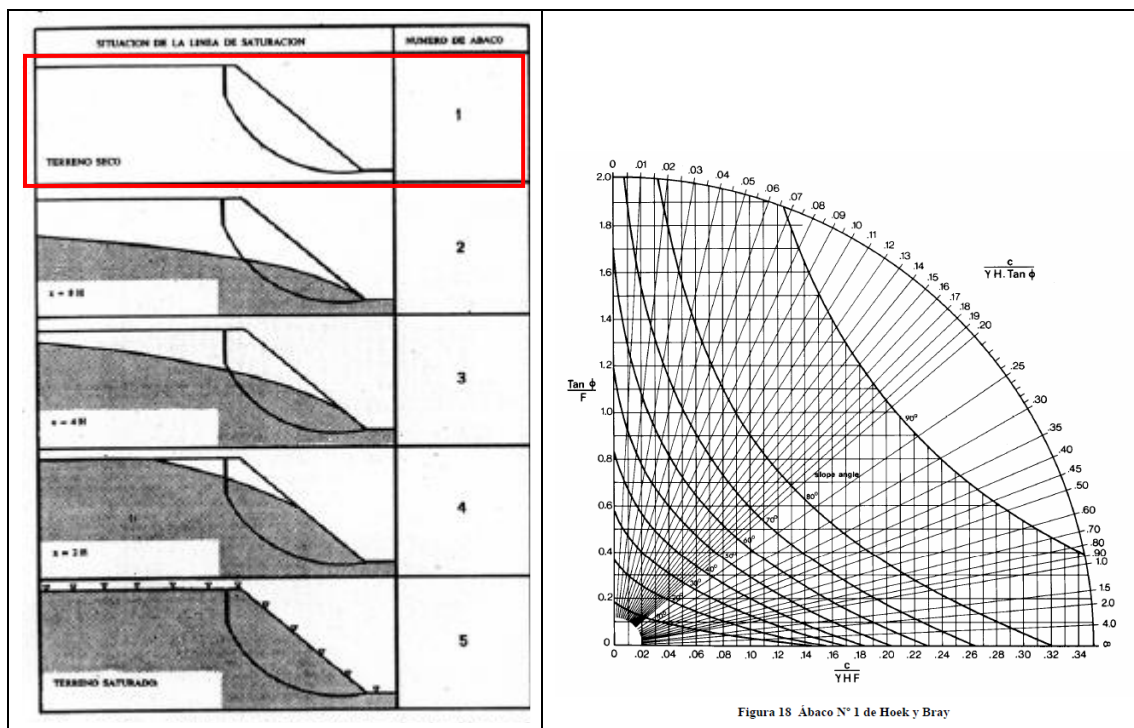


Figura 6 i Figura 7. Líneas de saturació possibles, es marca la que s'ha escollit. En la segona figura detall de l'àbac n°1 escollit.

Així per a tots aquests paràmetres exposant el vessant actual presenta factors de seguretat superiors a 3.5. Si els habitatges projectats es recolzen damunt dels materials del primer nivell de substrat, no suposaran una sobrecàrrega important damunt del vessant, i per tant, no modificarà substancialment els factors de seguretat del propi vessant, per tant amb valors sempre superior a 1.8, per tant complint les premisses marcades per part del CTE.



G3 D T S.L. sol·licita que si es detectessin anomalies respecte les dades que s'exposen, durant l'execució de la obra, agrairíem que ens avisessin, i igualment restem a la seva disposició per qualsevol consulta i/o dubte que vulguin realitzar, en el telèfon 973 33 12 12.

Informe geològic / geotècnic,
Expedient Núm.: 3001621

Els Omells de Na Gaia, 19 de novembre de 2025.



Desenvolupament Territorial S.L.
CIF B-25461443
C/ Església, 18 - Tel.973 33 12 12
25268 Els Omells de Na Gaia
(L'Urgell) Lleida

Eva Vázquez Marcet
Geòloga col 4302
Resp. Departament

BASE DE CÀLCUL



BASE DE CàLCUL

El procediment de càlcul utilitzat sempre comprèn els següents passos:

- Determinació de la tensió de trencament del terreny - per unes dimensions de sabates determinades.
- Càlcul de la tensió admissible, aplicant a l'anterior el coeficient de seguretat establert.
- Reajustament, si s'escau, de les dimensions de fonamentació.
- Càlcul dels assentaments previsibles.
- Modificació dels càlculs anteriors si els assentaments no són admissibles.

Tensió admissible

Un cop analitzat el procediment de càlcul i donat que partim de la premissa que els sòls sota la cota de fonamentació són heterogenis, a efectes de càlcul s'aplica el mètode que proposa el llibre de "*Curso aplicado de cimentaciones*", en el seu capítol 2, de J. Maria Rodríguez Ortiz y otros. En aquest llibre es proposen pel càlcul de tensions admissibles de fonamentacions superficials, ja sigui sabates aïllades, corregudes o llosa de fonamentació, els criteris de trencament dels terrenys bicapa.

Segons aquestes premisses es redueixen les diferents capes que es diferencien donada l'extensió de la superfície de trencament, a dues úniques capes, la reducció a aquesta segona capa es realitza amb la mitja ponderada de les diferents capes a considerar. S'aplicarà la profunditat de l'extensió de la superfície de trencament que es consideri més desfavorable.

Amb aquest mètode s'han de tenir en compte les pressions de trencament de la 1era capa i la 2ona capa, i aplicar les correccions que es donen segons quina sigui la relació entre les característiques de resistència de cada una de les dues capes considerades.

Pel càlcul de les tensions de trencament de cada una de les capes utilitzarem, i en el cas de caracteritzar les capes a partir de la seva *cohesió i angle de fregament intern*, i considerant *sabates corregudes*, la fórmula proposada per Terzaghi:



$$Q_d = C \cdot N_c + \gamma \cdot Z \cdot N_q + 0.5 \cdot \gamma \cdot B \cdot N_w$$

Pel càlcul de les tensions de trencament de cada una de les capes, i en el cas de caracteritzar les capes a partir de la seva *cohesió i angle de fregament intern*, i considerar *sabates aïllades*, la fórmula proposada per Terzaghi:

$$Q_d = 1.3 \cdot c \cdot N_c + \gamma \cdot Z \cdot N_q + 0.4 \cdot \gamma \cdot B \cdot N_w$$

on:

Q_d = Capacitat de càrrega límit (en Kg/m²).

c = Cohesió del sòl (en Kg/m²).

γ = Pes volumètric del sòl (en Kg/m³).

Z = Profunditat de desplant de la fonamentació (en m).

B = Ample de la sabata quadrada o dimensió menor de la sabata rectangular (en m).

N_c', **N_q'**, **N_w'** = factors de càrrega que s'obtenen a partir de l'angle de fregament intern (φ).

Pel càlcul de la tensió admissible en el cas de considerar un *terreny granular, sorrenc, o bé assimilable a aquestes característiques*, tindrem en compte els valors que s'obtenen de la N_{spt}, i a partir de les formules proposades per Terzaghi i Peck:

Per sabates < 1.2 m de costat

$$Q_{adm.} = N \times S / 8$$

Per sabates > 1.2 m de costat:

$$Q_{adm.} = N / 12 \times S / (B + 0.3) / B)^2$$

On:

N = Valor obtingut a partir de l'assaig SPT.

S = Valor de l'assentament admissible en polsades; S:1 (2.54 cm).

B = Ample de sabata en metres.



Assentaments

A partir de les consideracions de terrenys multicapa donats, en el mateix capítol del llibre citat, es proposen a partir del supòsit que estem davant de materials amb comportaments elàstics, un mètode pel càlcul d'assentaments que utilitza correlacions entre N, colpeig SPT, i el mòdul de deformació E.

El mètode de Schmertmann, suposa que els assentaments queden limitats a una profunditat de 2B, en el cas de sabates aïllades o llosa de fonamentació i 4B, en el cas de sabates corregudes.

Aquest mètode es basa en el sumatori de tots els assentaments que s'obtenen per cada una de les diferents capes definides i calculades a partir de la fórmula següent:

$$S = C_1 q \sum I / E - \Delta z$$

On:

C_1 = factor que depèn de l'empotrament de la sabata.

I = Coeficient d'influència que representa la relació de les tensions admissibles en profunditat.

E = mòdul de deformació definit per Schmertmann, que s'obté de multiplicar 2.5, en el cas de sabates aïllades i 3.5 en el cas de corregudes, pel colpeig del penetròmetre estàtic. Aquest colpeig s'obté de la relació entre N (N_{spt}), amb uns factors de conversió establerts per cada un dels diferents tipus de material.

Amb aquests valors que s'obté s'haurà de comprovar que els assentaments absoluts de cada una de les sabates és menor a 2.54 (1 polzada), en el cas de considerar sabates i menor a 5 cm (2 polzades), en el cas de considerar una llosa de fonamentació, que són els assentaments màxims admissibles establerts per a les estructures de formigó, segons Terzaghi.

REGISTRE D'ASSAIG MECANIC




ASSAIG DE PENETRACIÓ DINÀMICA: P-1 - 4 m (respecte el carrer).

OBRA: C/ ARBRELLS 18 A
DATA: 24/10/25

POBLACIÓ: CASTELLAR DEL VALLES
NÚMERO D'INFORME: 3001621

Gràfica de l'assaig de penetració

Profunditat de penetròmetre	Colpeig DPSH	Colpeig N _B	MOSTRA	N.F.	Nivells
0	0	0			
-0,2	0	0			
-0,4	6	7			
-0,6	10	12			
-0,8	13	16			
-1	38	46			
-1,2	100	120			
-1,4					
-1,6					
-1,8					
-2					
-2,2					
-2,4					
-2,6					
-2,8					
-3					
-3,2					
-3,4					
-3,6					
-3,8					
-4					
-4,2					
-4,4					
-4,6					
-4,8					
-5					
-5,2					
-5,4					
-5,6					
-5,8					
-6					
-6,2					
-6,4					
-6,6					
-6,8					
-7					
-7,2					
-7,4					
-7,6					
-7,8					
-8					
-8,2					
-8,4					
-8,6					
-8,8					
-9					
-9,2					
-9,4					
-9,6					
-9,8					
-10					
-10,2					
-10,4					
-10,6					
-10,8					
-11					
-11,2					
-11,4					
-11,6					
-11,8					
-12					

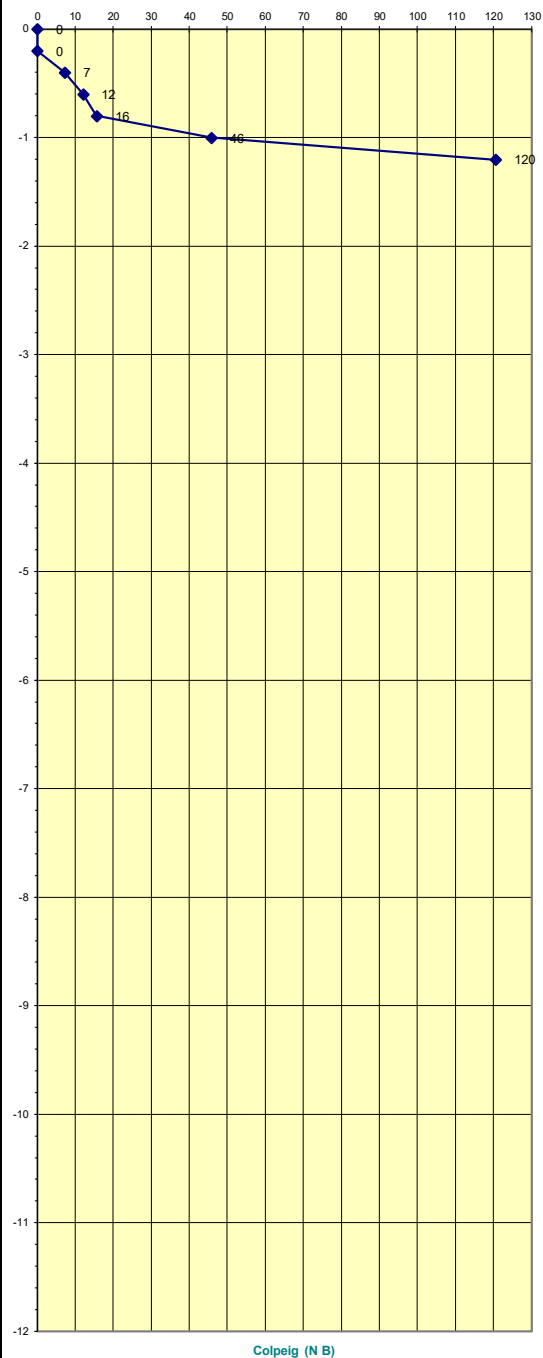

Nivell 1
Rebuig a -1,08 m




ASSAIG DE PENETRACIÓ DINÀMICA: P-2 cota inici: -4,2 m (respecte el carrer)

OBRA: C/ ARBRELLS 18 A
DATA: 24/10/25

POBLACIÓ: CASTELLAR DEL VALLES
NÚMERO D'INFORME: 3001621

Gràfica de l'assaig de penetració

Profunditat de penetròmetre	Colpeig DPH	Colpeig N _B	MOSTRA	N.F.	Nivells
0	0	0			
-0,2	0	0			
-0,4	15	18			
-0,6	100	120			
-0,8					
-1					
-1,2					
-1,4					
-1,6					
-1,8					
-2					
-2,2					
-2,4					
-2,6					
-2,8					
-3					
-3,2					
-3,4					
-3,6					
-3,8					
-4					
-4,2					
-4,4					
-4,6					
-4,8					
-5					
-5,2					
-5,4					
-5,6					
-5,8					
-6					
-6,2					
-6,4					
-6,6					
-6,8					
-7					
-7,2					
-7,4					
-7,6					
-7,8					
-8					
-8,2					
-8,4					
-8,6					
-8,8					
-9					
-9,2					
-9,4					
-9,6					
-9,8					
-10					
-10,2					
-10,4					
-10,6					
-10,8					
-11					
-11,2					
-11,4					
-11,6					
-11,8					
-12					

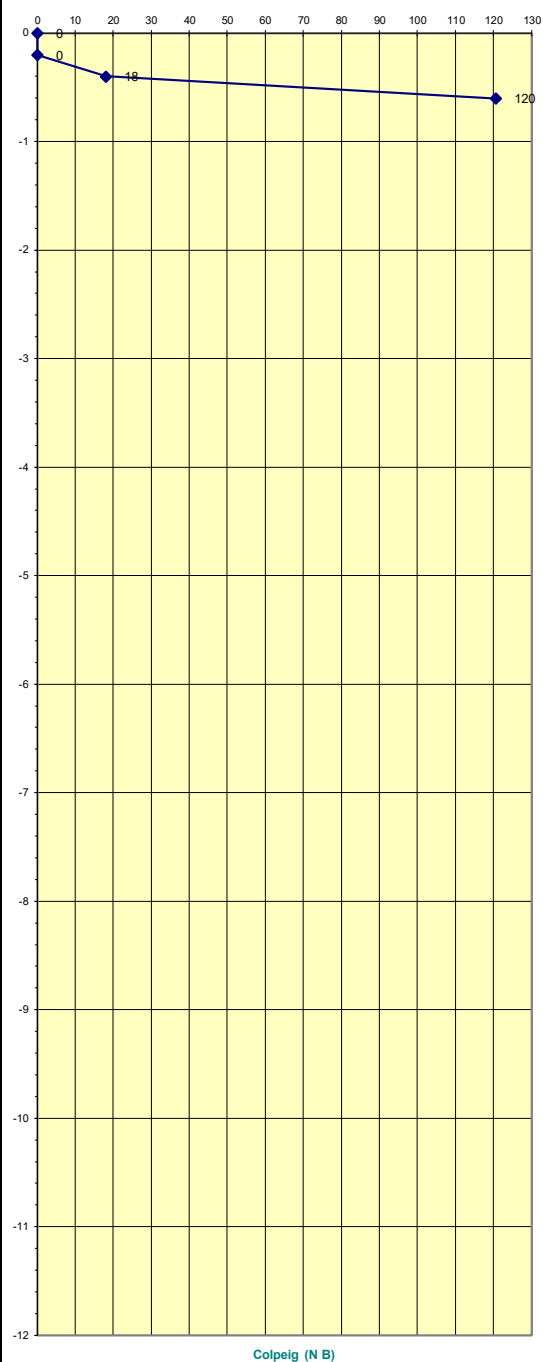

Nivell 1
Rebuig a -0,48 m




ASSAIG DE PENETRACIÓ DINÀMICA: P-3 cota inici: - 4 m (respecte el carrer).

OBRA: C/ ARBRELLS 18 A
DATA: 24/10/25

POBLACIÓ: CASTELLAR DEL VALLES
NÚMERO D'INFORME: 3001621

Gràfica de l'assaig de penetració

Profunditat de penetròmetre	Colpeig DPSH	Colpeig N _B	MOSTRA	N.F.	Nivells
0	0	0			
-0,2	0	0			
-0,4	16	19			
-0,6	46	55			
-0,8	100	120			
-1					
-1,2					
-1,4					
-1,6					
-1,8					
-2					
-2,2					
-2,4					
-2,6					
-2,8					
-3					
-3,2					
-3,4					
-3,6					
-3,8					
-4					
-4,2					
-4,4					
-4,6					
-4,8					
-5					
-5,2					
-5,4					
-5,6					
-5,8					
-6					
-6,2					
-6,4					
-6,6					
-6,8					
-7					
-7,2					
-7,4					
-7,6					
-7,8					
-8					
-8,2					
-8,4					
-8,6					
-8,8					
-9					
-9,2					
-9,4					
-9,6					
-9,8					
-10					
-10,2					
-10,4					
-10,6					
-10,8					
-11					
-11,2					
-11,4					
-11,6					
-11,8					
-12					

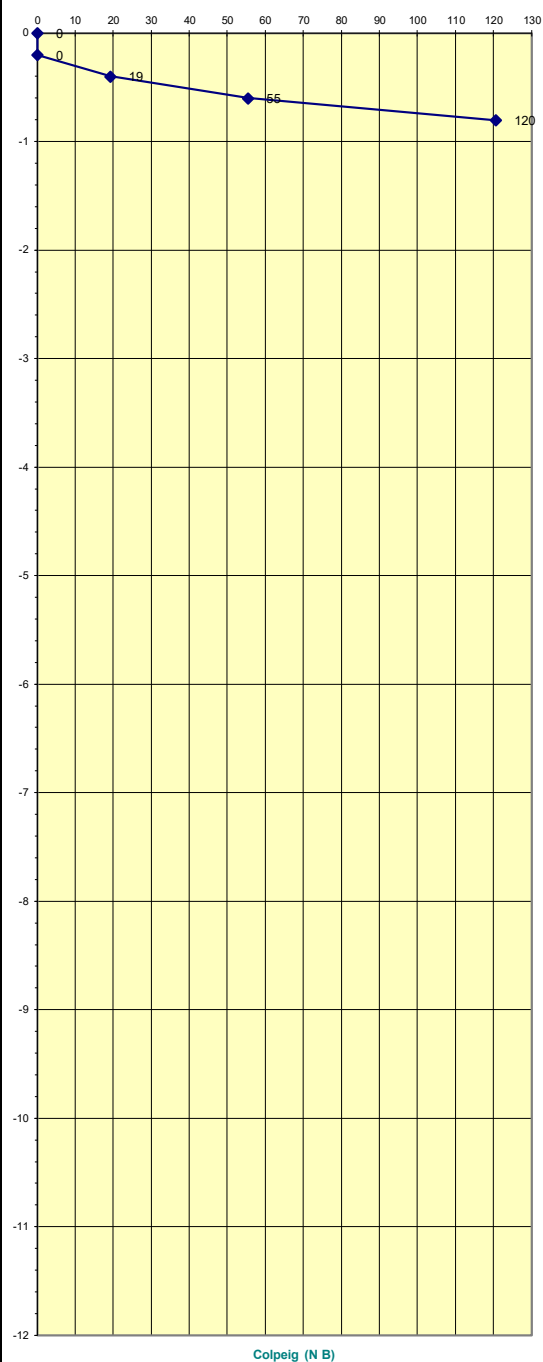

Nivell 1
Rebuig a -0,76 m




ASSAIG DE PENETRACIÓ DINÀMICA: P-4 - 4 m (respecte el carrer).

OBRA: C/ ARBRELLS 18 A
DATA: 24/10/25

POBLACIÓ: CASTELLAR DEL VALLES
NÚMERO D'INFORME: 3001621

Gràfica de l'assaig de penetració

Profunditat de penetròmetre	Colpeig DPSH	Colpeig N _B	MOSTRA	N.F.	Nivells
0	0	0			
-0,2	0	0			
-0,4	8	10			
-0,6	8	10			
-0,8	12	14			
-1	27	33			
-1,2	21	25			
-1,4	28	34			
-1,6	100	120			
-1,8					
-2					
-2,2					
-2,4					
-2,6					
-2,8					
-3					
-3,2					
-3,4					
-3,6					
-3,8					
-4					
-4,2					
-4,4					
-4,6					
-4,8					
-5					
-5,2					
-5,4					
-5,6					
-5,8					
-6					
-6,2					
-6,4					
-6,6					
-6,8					
-7					
-7,2					
-7,4					
-7,6					
-7,8					
-8					
-8,2					
-8,4					
-8,6					
-8,8					
-9					
-9,2					
-9,4					
-9,6					
-9,8					
-10					
-10,2					
-10,4					
-10,6					
-10,8					
-11					
-11,2					
-11,4					
-11,6					
-11,8					
-12					

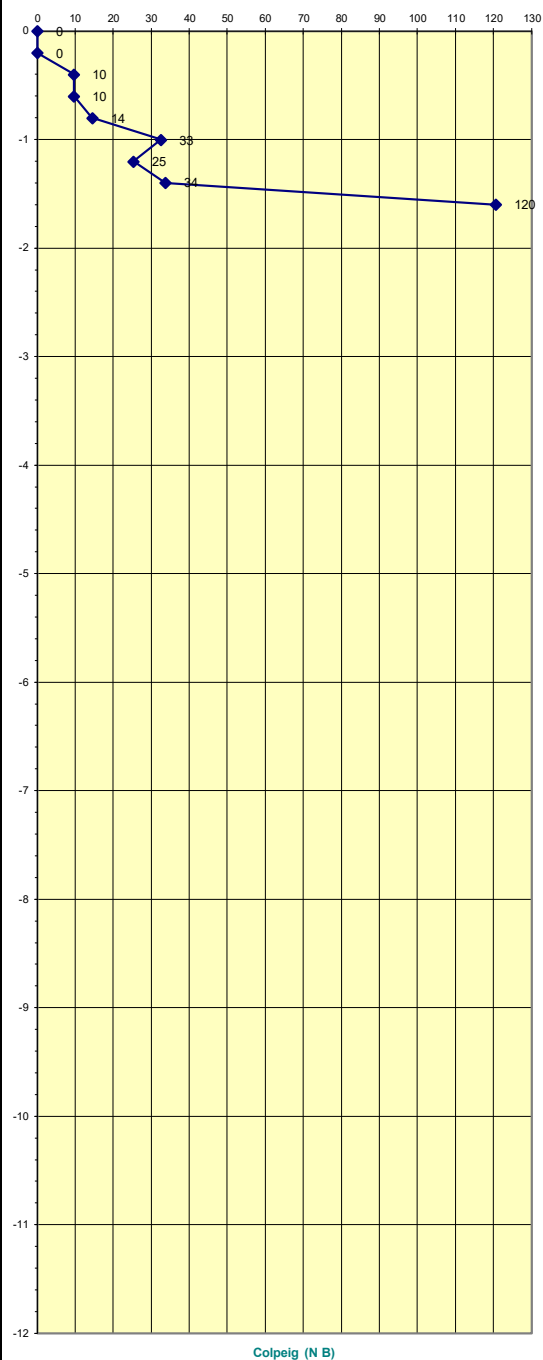

	Nivell 1
	Rebuig a -1,55 m

Sondeig a rotació amb bateria continua



Sondeig nº:	S-1	Client:	WOOD COMFORT PROM.	Màquina:	ML76A
Obra:	ESTUDI GEOLÒGIC I GEOTÈCNIC PER A LA CONSTRUCCIÓ D'UNA HABITATGE UNIFAMILIAR AÏLLATAL CARRER ARBRELLS Nº 18A-18B-20, CASTELLAR DEL VALLÈS (BARCELONA).	Data d'inici:	24/10/25	Empresa:	TPS
		Data de fi:	24/10/25	Sondista:	Sr. DANIEL FERNÁNDEZ

Sondeig nº:	S-1	Client:	WOOD COMFORT PROM.	Màquina:	ML76A
Obra:	ESTUDI GEOLÒGIC I GEOTÈCNIC PER A LA CONSTRUCCIÓ D'UNA HABITATGE UNIFAMILIAR AÏLLATAL CARRER ARBRELLS Nº 18A-18B-20, CASTELLAR DEL VALLÈS (BARCELONA).	Data d'inici:	24/10/25	Empresa:	TPS
		Data de fi:	24/10/25	Sondista:	Sr. DANIEL FERNÁNDEZ

<i>Data de fi:</i>	24/10/25
--------------------	----------

Sondista: Sr. DANIEL FERNÁNDEZ

<i>UTM:</i>	423182.0 E(x) 4609623.0 N(y)
<i>Cota (Z):</i>	570.90 msnm (segons el plànol ICGC)

Tècnic:

Eva Vázquez Marcet
Geòloga col 4302

[illegible]

Observacions:	
---------------	--

Sondeig a rotació amb bateria continua



Sondeig nº: S-1

Obra: ESTUDI GEOLÒGIC I GEOTÈCNIC PER A LA CONSTRUCCIÓ D'UNA HABITATGE UNIFAMILIAR AÏLLATAL CARRER ARBRELLS Nº 18A-18B-20, CASTELLAR DEL VALLÈS (BARCELONA).

Client: WOOD COMFORT PROM.

Data d'inici: 24/10/25

Data de fi: 24/10/25

Màquina: ML76A

Empresa: TPS


Sondista: Sr. DANIEL FERNÁNDEZ

UTM: 423182.0 E(x)
4609623.0 N(y)

Cota (Z): 570.90 msnm (segons el plànol ICGC)

Tècnic:

Eva Vázquez Marcet
Geòloga col 4302

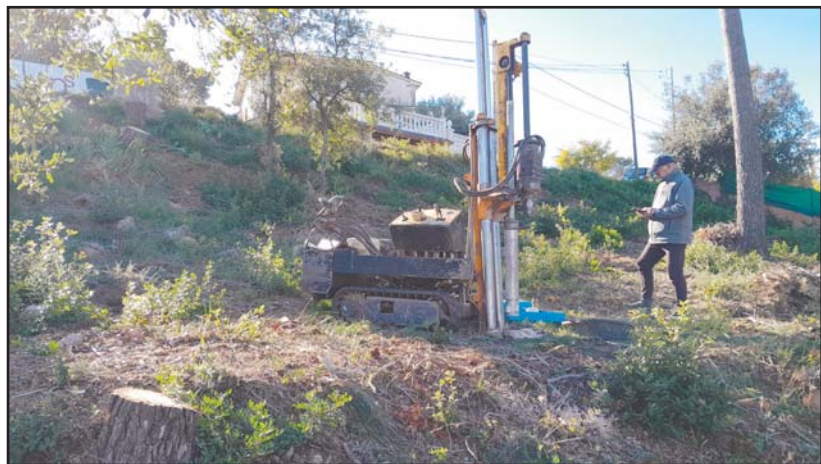

Fotografia 1. Vista de l'emplaçament de la màquina per a la realització del sondeig a rotació amb bateria continua S-1.



Fotografia 2. Material recuperat en el sondeig S-1 entre les cotes de 0.00 a -1.20 metres de profunditat.



ESQUEMA DE SITUACIÓ DELS ASSAIGS



TÍTOL DEL PROJECTE

ESTUDI GEOLÒGIC I GEOTÈCNIC PER A LA CONSTRUCCIÓ D'UNA HABITATGE UNIFAMILIAR AÏLLAT
AL CARRER ARBRELLS Nº 18A-18B-20, CASTELLAR DEL VALLÈS (BARCELONA).

Data: Octubre 2025

Exp: 3001621

Plànol de situació


Pàgina 1/1

TALL DE CORRELACIÓ



LLEGENDA

-  Terreny Vegetal. Llims argilosos de color marró fosc amb graves i algunes arrels.
-  **Nivell 1:** Substrat rocós. Bretxes amb intercalacions de lutites i gresos vermells.
-  Cota de fonamentació recomanada

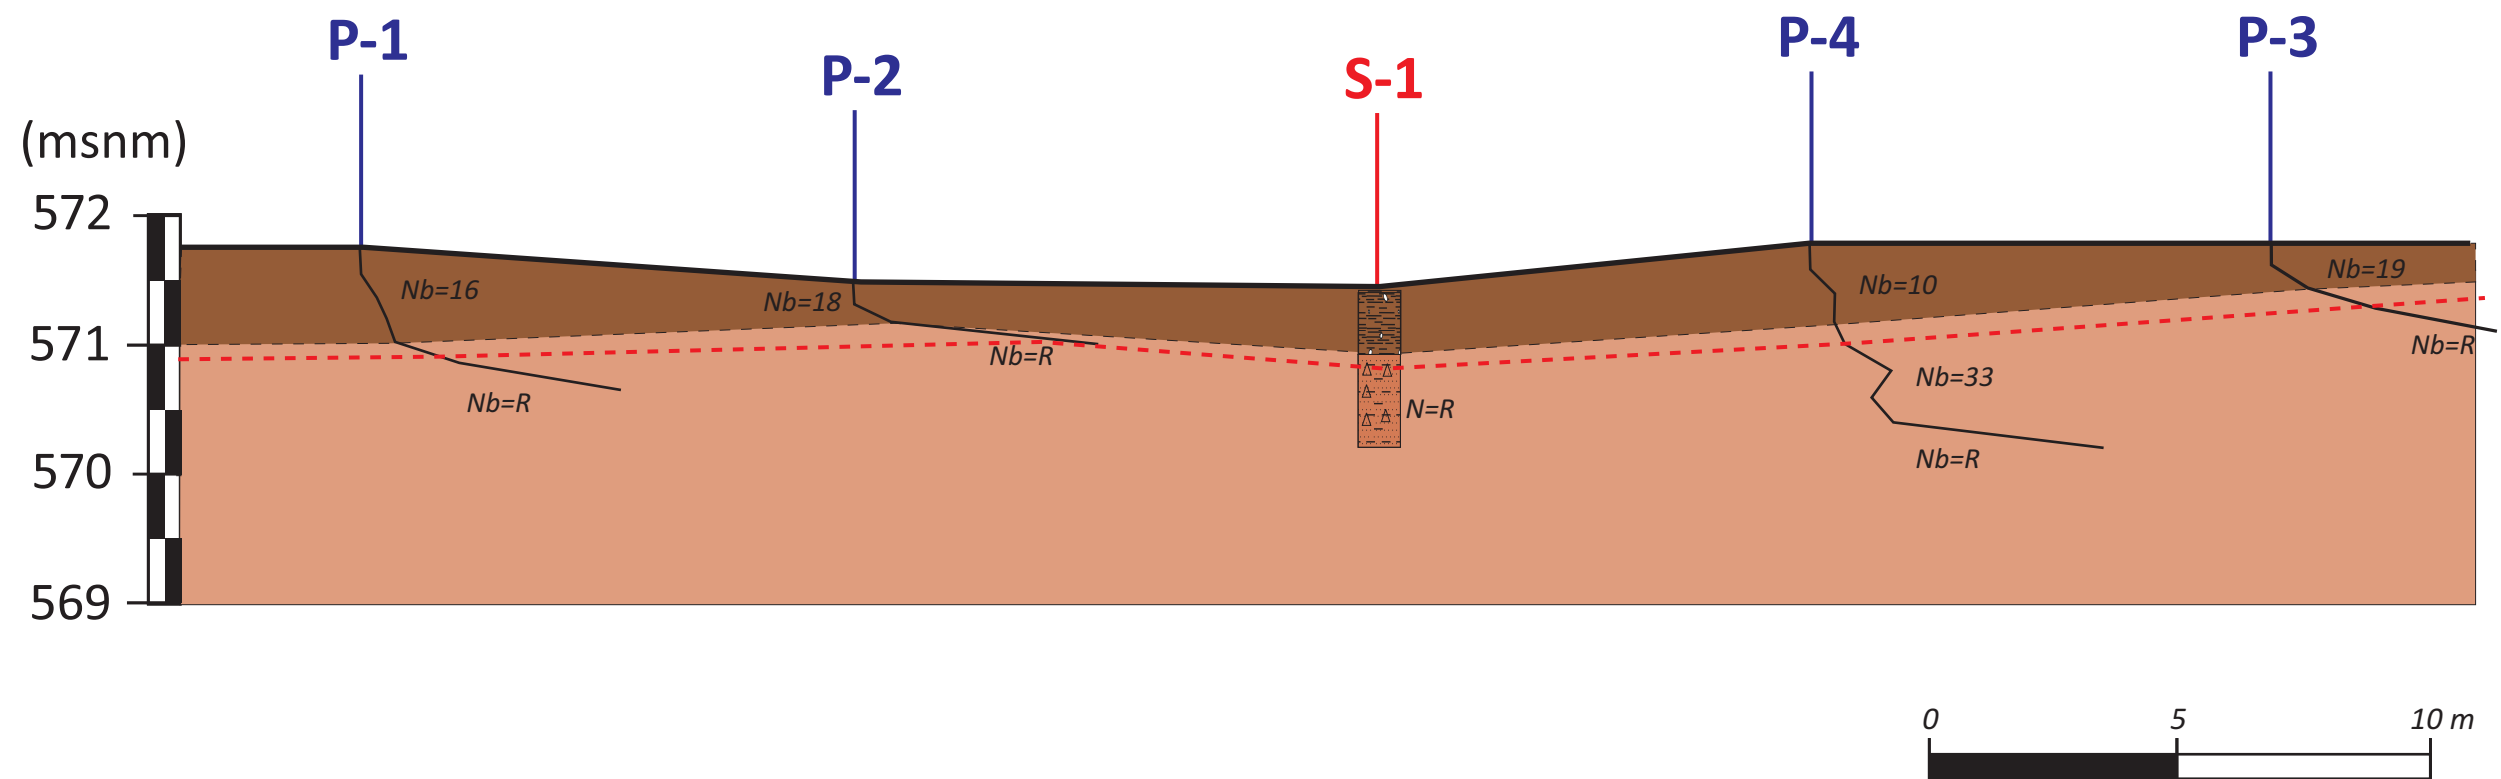

TÍTOL DEL PROJECTE

ESTUDI GEOLÒGIC I GEOTÈCNIC PER A LA CONSTRUCCIÓ D'UNA HABITATGE UNIFAMILIAR AÏLLAT
AL CARRER ARBRELLS Nº 18A-18B-20, CASTELLAR DEL VALLÈS (BARCELONA).

Data: Octubre 2025

Exp: 3001621

Tall de correlació

Pàgina 1/1


FOTOGRAFIES



Fotografia 1 -2: Detall de l'emplaçament de la màquina realitzant l'assaig de penetració dinàmica DPSH, P-1 i P-2, respectivament.



F-3

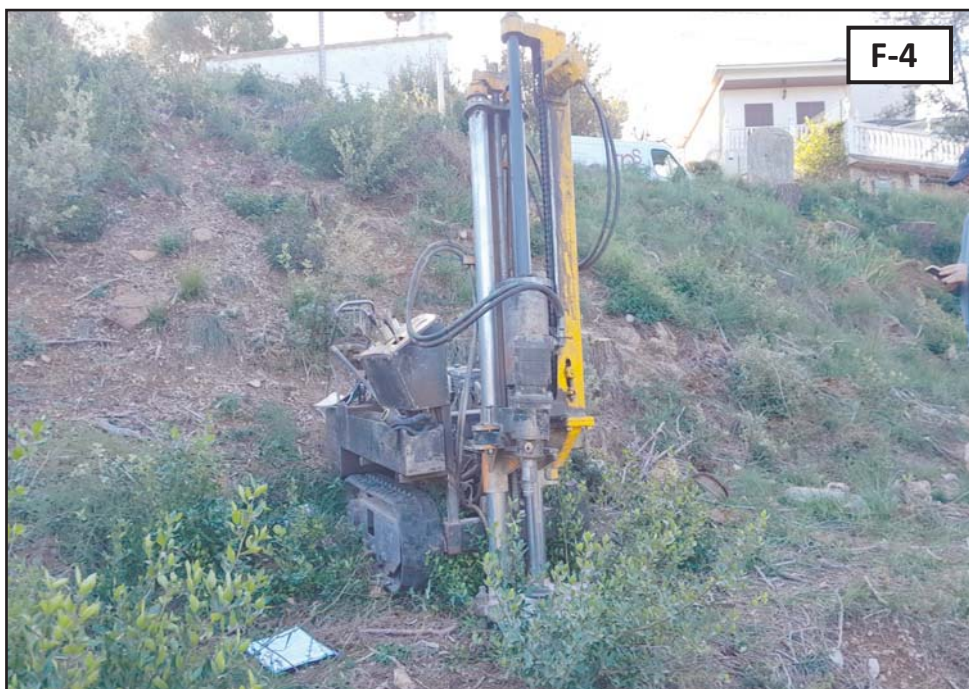

F-4

Fotografia 3 -4: Detall de l'emplaçament de la màquina realitzant l'assaig de penetració dinàmica DPSH, P-3 i P-4, respectivament.

ACTES D'ASSAIGS DE LABORATORI

INFORME DE RESULTATS D'ASSAIGS DE LABORATORI

Número d'informe: 4687-GTL-25

Data d'expedició: 19/11/2025

DADES DEL CLIENT:

Codi client: 0001

Nom: G3 Desenvolupament Territorial, SL

NIF: B25364589

Adreça: C/ Vallbona núm. 22 - 25268 Els Omells de Na Gaia (Lleida)

MATERIAL A ASSAJAR:

Tipus de mostra/es: Sòl

Situació: Castellar del Vallés. Carrer Arbrells.

Referència/es del laboratori: GTL-8230-25

Les dades expressades en el present informe fan referència única i exclusivament als resultats obtinguts en els assaigs realitzats en cadascuna de les mostres referenciades. El laboratori no es responsabilitza de qualsevol extrapolació o associació dels resultats obtinguts a altres mostres que no hagin estat degudament assajades.

OBERTURA, PREPARACIÓ I DESCRIPCIÓ DE LA MOSTRA

Número d'informe: 4687-GTL-25

UNE 103100:95

Data d'expedició: 19/11/2025

Mostra: GTL-8230-25

DADES DEL SOL.LICITANT:

Nom: G3 Desenvolupament Territorial, SL

NIF: B25364589

Adreça: C/ Vallbona núm. 22 - 25268 Els Omells de Na Gaia (Lleida)

DADES INICIALS:

Mostra: MA1 S1

Cota d'extracció (m): 1,0 - 1,2

Tipus de mostra: Alterada

Tipus de material: Sòl

Obra / Projecte: Castellar del Vallés. Carrer Arbrells. 3001621

Emmagatzematge: Cambra humida

Sistema d'obertura: Manual

Dimensions de la mostra:

Alçada (mm): -

Data extracció: 24/10/2025

Diàmetre (mm): -

Data recepció: 24/10/2025

Data obertura: 24/10/2025

DESCRIPCIÓ DEL MATERIAL:

Grava amb llims

ASSAIGS REALITZATS:

Determinació del contingut en ió sulfat en sòls UNE 83963 / 08

OBSERVACIONS:

Núm. Informe: 4687-GTL-25

ASSAIGS QUÍMICS EN SÒLS

Número d'informe: 4687-GTL-25

Data d'expedició: 19/11/2025

Mostra: GTL-8230-25

Determinació del contingut en ió sulfat en sòls - UNE 83963 : 2008

Massa de sòl analitzada	25,0	g
Contingut en SO_4^{2-}	0,0	mg/kg

Data de realització: 18/11/2025

Operador: PC

OBSERVACIONS:

Núm. Informe: 4687-GTL-25

RESUM DELS RESULTATS OBTINGUTS

Número d'informe: 4687-GTL-25

Data d'expedició: 19/11/2025

ASSAIGS EN MOSTRES DE SÒLS I ROQUES

ASSAIGS EN MOSTRES DE SÒLS I ROQUES								
MOSTRA	Referència del laboratori		GTL-8230-25					
	Referència del client		MA1 S1					
	Tipus de material		Sòl					
	Cota d'extracció (m)		1,0 - 1,2					
GRANULOMÈTRIC PER TAMISSAT	% que passa el tamís 5 mm UNE							
	% que passa el tamís 2 mm UNE							
	% que passa el tamís 0,4 mm UNE							
	% que passa el tamís 0,08 mm UNE							
	Cu							
LÍMITS D'ATTERBERG	Cc							
	Límit líquid							
	Límit plàstic							
Índex de plasticitat								
CLASSIFICACIÓ SUCS								
HUMITAT NATURAL (%)								
DENSITAT	Densitat aparent (g/cm³)							
	Densitat seca (g/cm³)							
DENSITAT RELATIVA PARTÍCULES SÒLIDES (g/cm³)								
INFLAMENT LLIURE (%)								
PRESSIÓ D'INFLAMENT	Pressió màx. d'inflament (kp/cm²)							
	Inflament en descàrrega (%)							
ASSAIG LAMBE	Índex d'inflament (MPa)							
	Canvi potencial de volum							
COL·LAPSE EN SÒLS	Índex de col·lapse, I (%)							
	Pot. Perc. de col·lapse, I _c (%) (%)							
CONSOLIDACIÓ EN EDÒMETRE	e ₀ , índex de porus inicial							
	e _r , índex de porus final							
COMPRESSIÓ UNIAXIAL EN MOSTRES DE SÒL	Resistència (kp/cm²)							
	Deformació (%)							
COMPRESSIÓ UNIAXIAL EN MOSTRES DE ROCA	Resistència (kp/cm²)							
	(KPa)							
TALL DIRECTE	Φ (°)							
	C _u (kg/cm²)							
	Φ '(°)							
	C' (kg/cm²)							
	Φ' residual (°)							
PROCTOR MODIFICAT	C' residual (kg/cm²)							
	Densitat seca màxima (g/cm³)							
ASSAIG CBR	Humitat òptima (%)							
	Índex CBR	25 % Energia						
		50 % Energia						
100 % Energia								
ASSAIG TILT TEST	Φ _b (°)							
CONTINGUT EN MATÈRIA ORGÀNICA OXIDABLE (%)								
CONTINGUT EN GUIXOS D'UN SÒL (%)								
CONTINGUT EN SAL SOL·LUBLES D'UN SÒL (mg/kg de mostra)								
CONTINGUT EN IÓ SULFAT	mg de SO ₄ /kg de mostra		0,0					
GRAU D'ACIDES BAUMANN-GULLY (ml/kg mostra)								
GRAU D'AGRESSIVITAT DEL SÒL								

ASSAIGS EN MOSTRES D'AIGUA

DETERMINACIÓ DEL PH								
CONTINGUT RESIDU SEC (mg /l de mostra)								
CONTINGUT EN CO ₂ AGRESSIU (mg CO ₂ /l de mostra)								
CONTINGUT EN IÓ AMONI (mg NH ₄ /l de mostra)								
CONTINGUT EN IÓ SULFAT (mg SO ₄ /l de mostra)								
CONTINGUT EN IÓ MAGNESI (mg Mg ²⁺ /l de mostra)								
GRAU D'AGRESSIVITAT DE L'AIGUA								

Núm. Informe: 4687-GTL-25

INFORME DE RESULTATS D'ASSAIGS DE LABORATORI

Número d'informe: 4687-GTL-25

Data d'expedició: 19/11/2025

DADES DEL CLIENT:

Codi client: 0001

Nom: G3 Desenvolupament Territorial, SL

NIF: B25364589

Adreça: C/ Vallbona núm. 22 - 25268 Els Omells de Na Gaia (Lleida)

MATERIAL ASSAJAT:

Tipus de mostra/es: Sòl

Situació: Castellar del Vallés. Carrer Arbrells.

Referència/es del laboratori: GTL-8230-25



Firmado digitalmente por
CERVOS FLINCH,
PERE (FIRMA)
Fecha: 2025.11.19
13:12:39 +01'00'

Pere Cervós Flinch

Geòleg col 5326

Cap d'àrea d'assaig GTL



Firmado digitalmente por Pere
Farres Bori
Nombre de reconocimiento (DN):
cn=Pere Farres Bori, o=TPS,
Prospecció del Subsòl, ou=Tecnic,
email=pfarres@tps-
perforaciones.com, c=ES
Fecha: 2025.11.19 15:05:43 +01'00'
Versión de Adobe Acrobat:
2015.007.00000

Pere Farrés i Bori

Geòleg col. Núm.: 3481

Director tècnic