




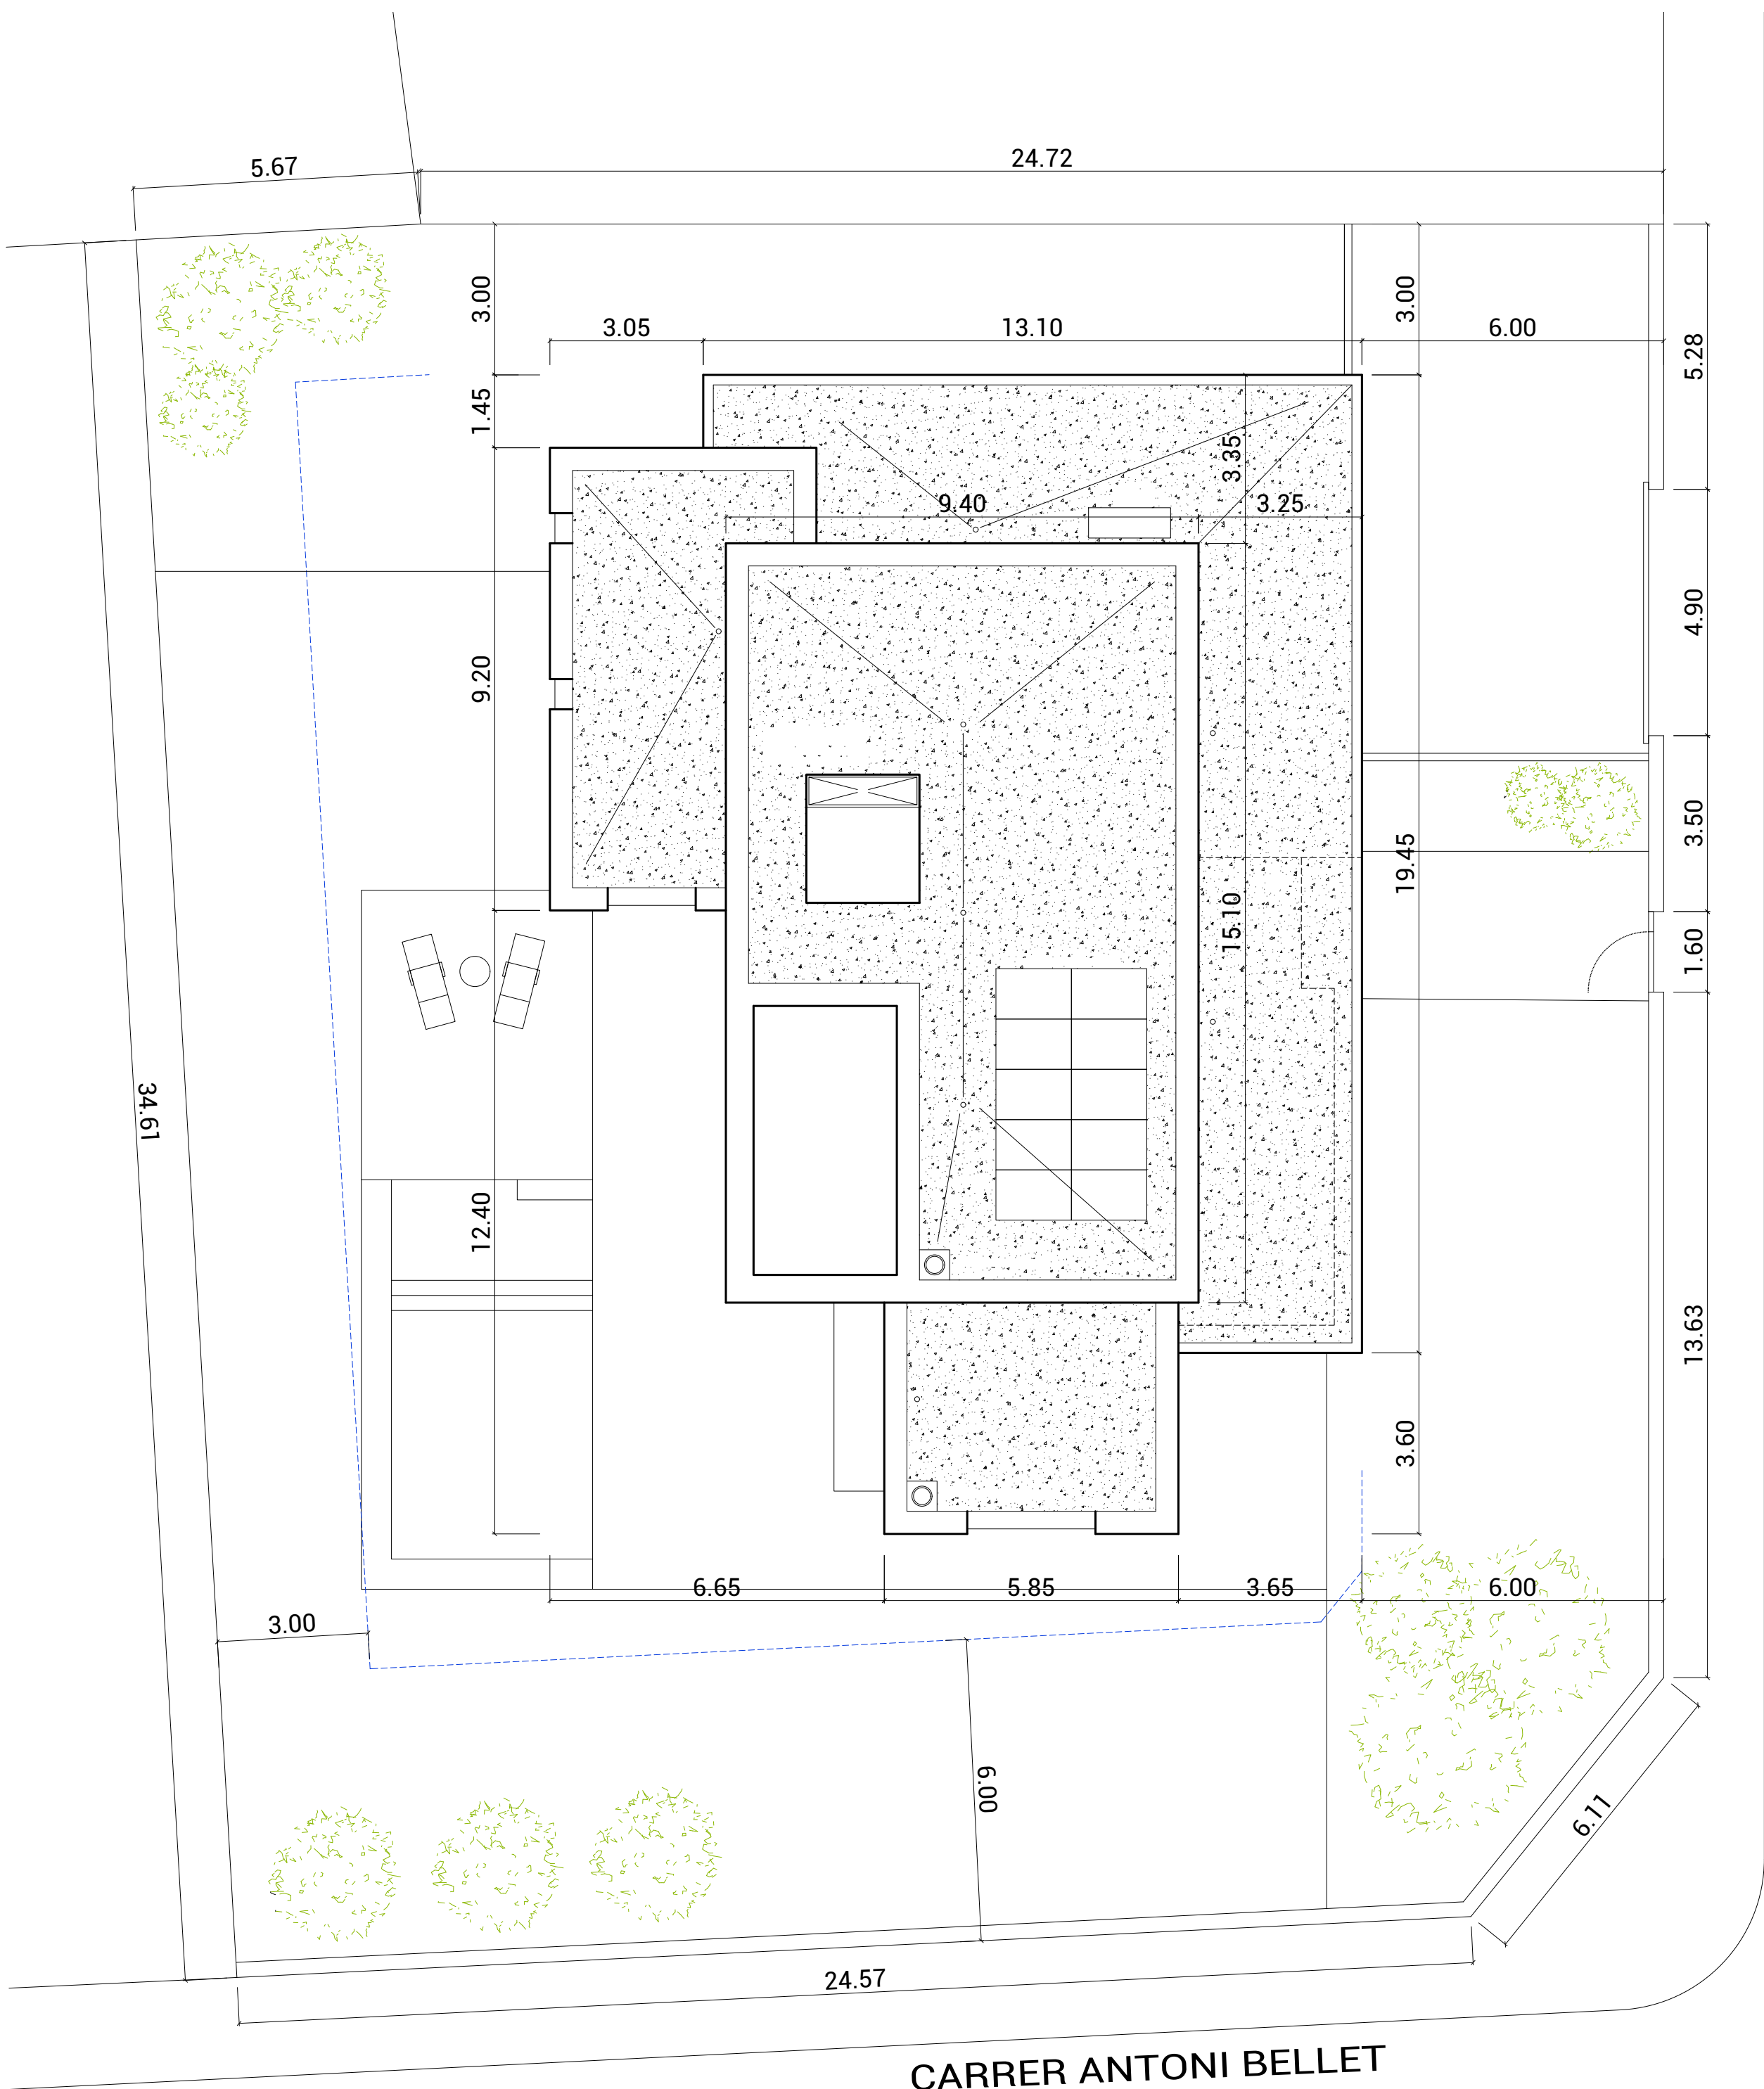


PLANTA COBERTA
E. 1/100

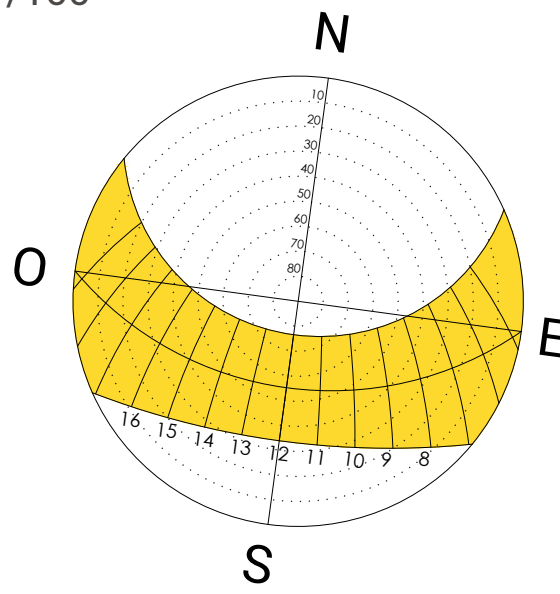

AEREA
E. 1/750

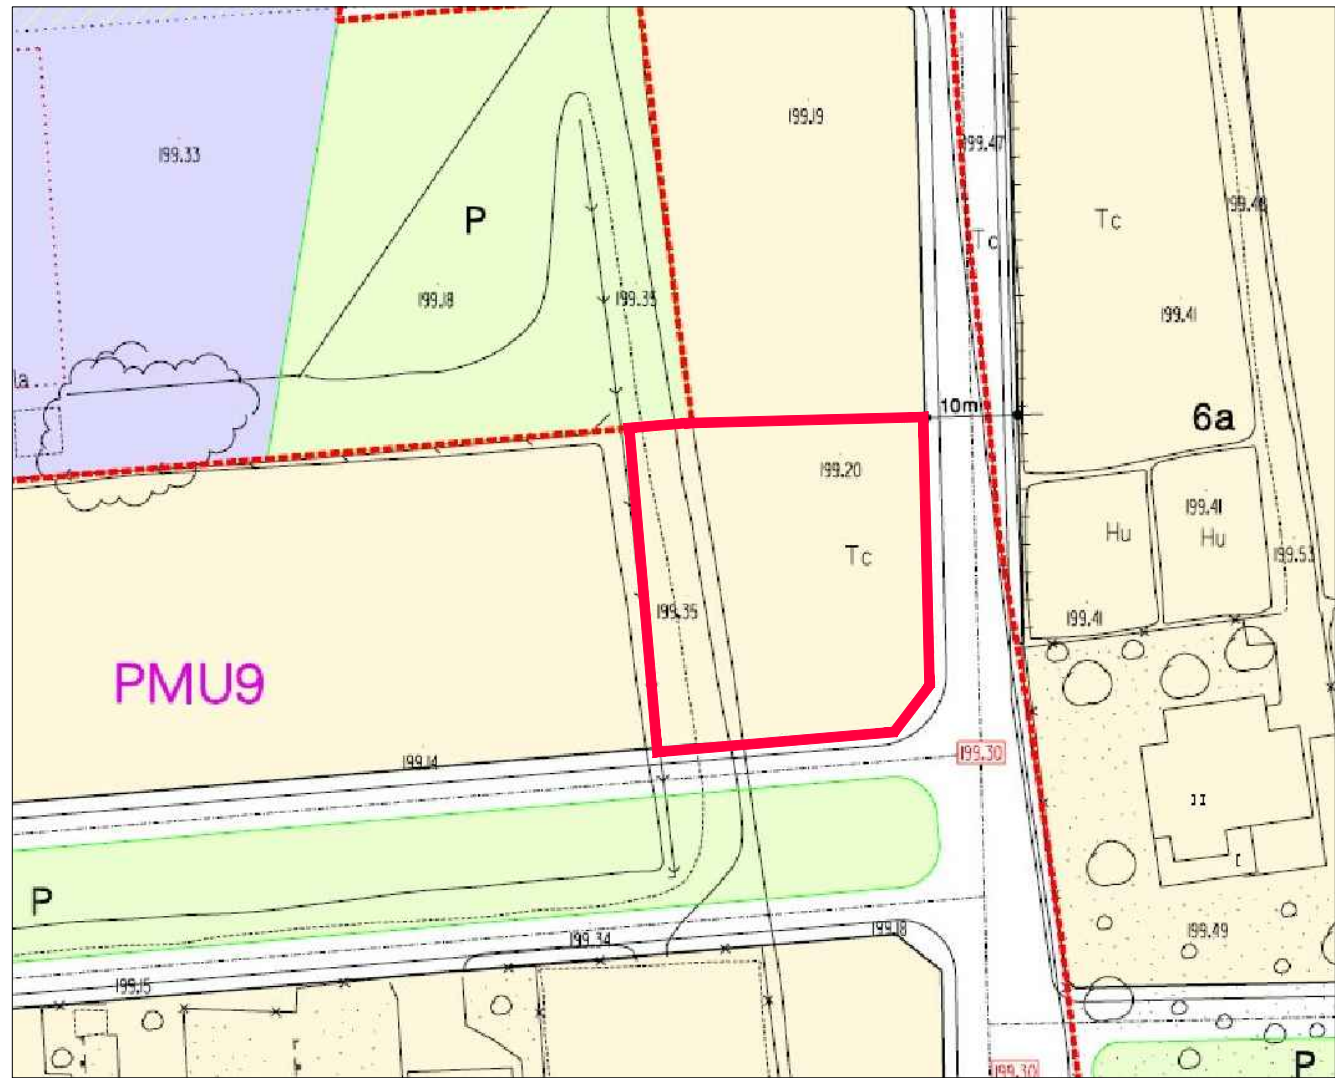

CARRER MESTRE RAMON ORTIZ

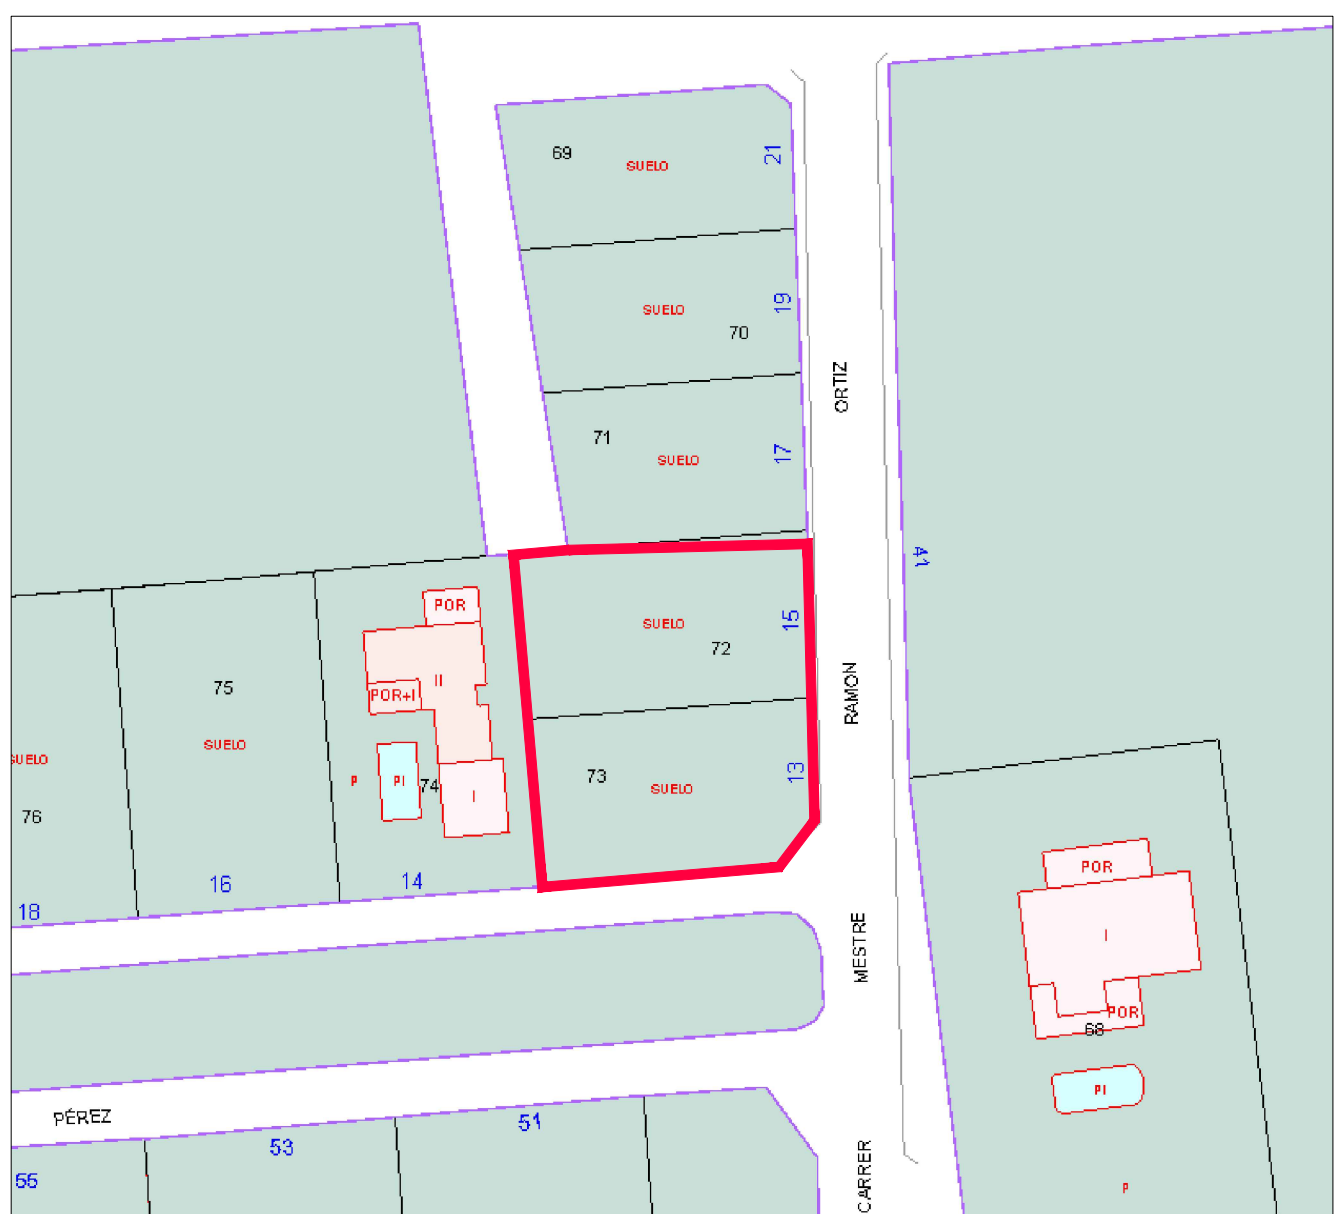

CATASTRE
E. 1/750



AEREA
E. 1/500

CARRER ANTONI BELLET

JUSTIFICACIO PLANEJAMENT

Ordenació urbanística	POUM Bell-lloc d'Urgell PLA MILLORA URBANA PMU-9	
Classificació i règim del sòl	SOL URBA. Edificació aïllada unifamiliar	
Classificació del sòl	CLAU-6. MpPOUM (aprovat CTULL 26.02.2020)	
Qualificació urbanística		
Tipus d'ordenació	Planejament	Projecte
Parcel·la mínima	Aïllada	Aïllada
Façana mínima	CLAU 6B min 600.00 m2	995.00m2
Ocupació	15 mts	24.07 mts
Gàl·lib front-fons-lateral	CLAU 6B 30% (298,50 m2 max)	296.80 m2
H. max	CLAU 6B 6-3-3 (carrer-lateral-fons)	6-3-3
N. plantes	CLAU 6B 0.4m2st/m2s (398,00 m2 màx)	6.50 m
IEN	PB+PP	PB+PP
Tanca	CLAU 6B 0.4m2st/m2s (398,00 m2 màx)	397,00 m2
	H.màx 1.60m (0.60m massís + resta vegetal)	Compleix

abn ARQUITECTURA
BOSCH NOVELL

Projecte Bàsic i Executiu

HABITATGE UNIFAMILIAR
AÏLLAT

Situació
CARRER MESTRE RAMON ORTIZ
25220 BELL-LLOC D'URGELL (Lleida)

Plànol
A.01
ARQUITECTURA
Emplaçament i situació

Promotor
RAMON MITJANA SL

Arquitecte
Jordi Bosch Novell