





provincia: LLEIDA
comarca: PLA URGELL
municipi: LINYOLA
població: LINYOLA
altitud: 720m

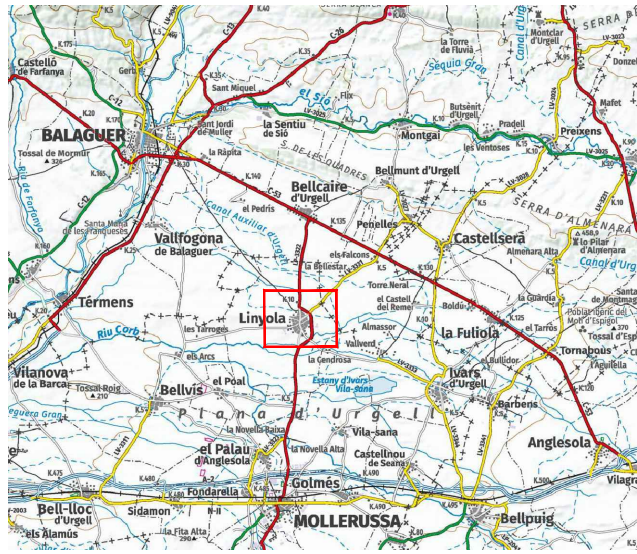

SITUACIÓ GENERAL



ORTOFOTO

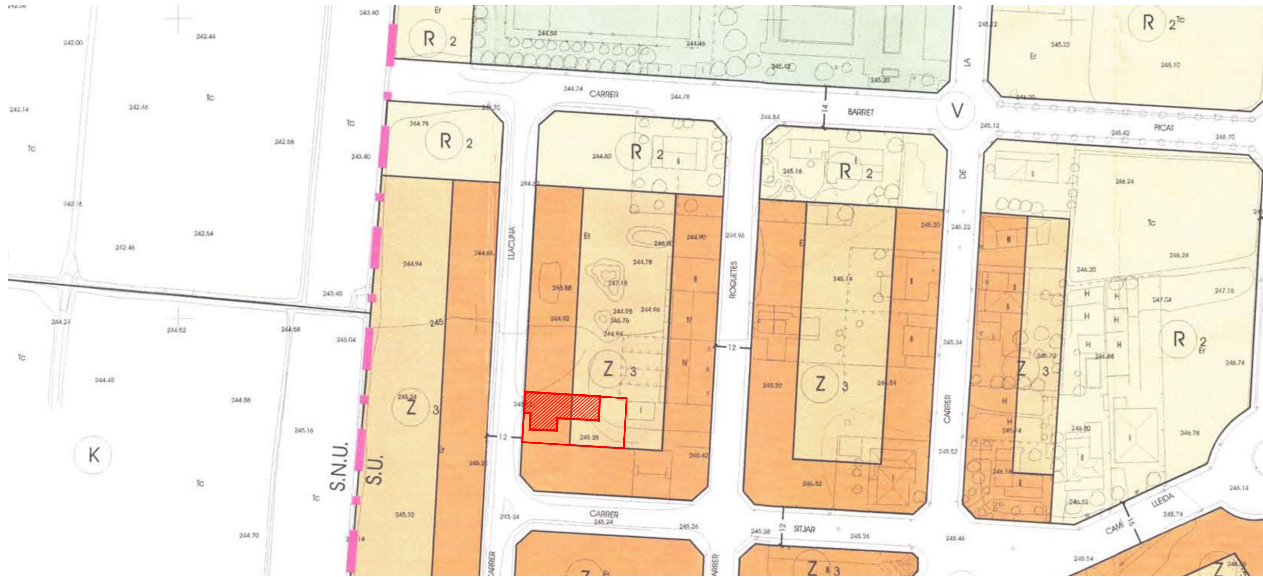

PLA D'ORDENACIÓ URBANÍSTICA MUNICIPAL

NORMATIVA URBANÍSTICA


NORMES SUBSIDIARIES DE PLANEJAMENT, Text refós Gener 2002 - LINYOLA

PARÀMETRES NORMATIVA _ 5098344CG2159N0000US
CLASSIFICACIÓ DEL SÒL: SU – sòl urbà
ZONA: Ordenació segons alineació a vial – clau Z
ÚS: residencial


FORMA ORDENACIÓ
alineació a vial o carrer
PARCEL·LA MÍNIMA: 150m²
OCUPACIÓ PB: 100%
PROFUNDITAT EDIFICABLE: dist. entre vials menor 30m
100%
FRONAT MÍN. PARCEL·LA 4,50m
FONDÀRIA MÍN. PARCEL·LA 10,00m
NOMBRE MAXIM PLANTES: PB+2PP
ALÇADA REGULADORA MAX.: 11,00m
COBERTA: inclinada
PENDENT COBERTA: màxim 30%


PROJECTE

FORMA ORDENACIÓ
alineació a vial o carrer
PARCEL·LA MÍNIMA: 571m²
OCUPACIÓ: 41,33%
PROFUNDITAT EDIFICABLE: 25,00m
FRONAT MÍN. PARCEL·LA 16,83m
FONDÀRIA MÍN. PARCEL·LA 34,00m
NOMBRE MAXIM PLANTES: PB
ALÇADA REGULADORA MAX.: 3,48m
COBERTA: inclinada i plana
PENDENT COBERTA: 30%

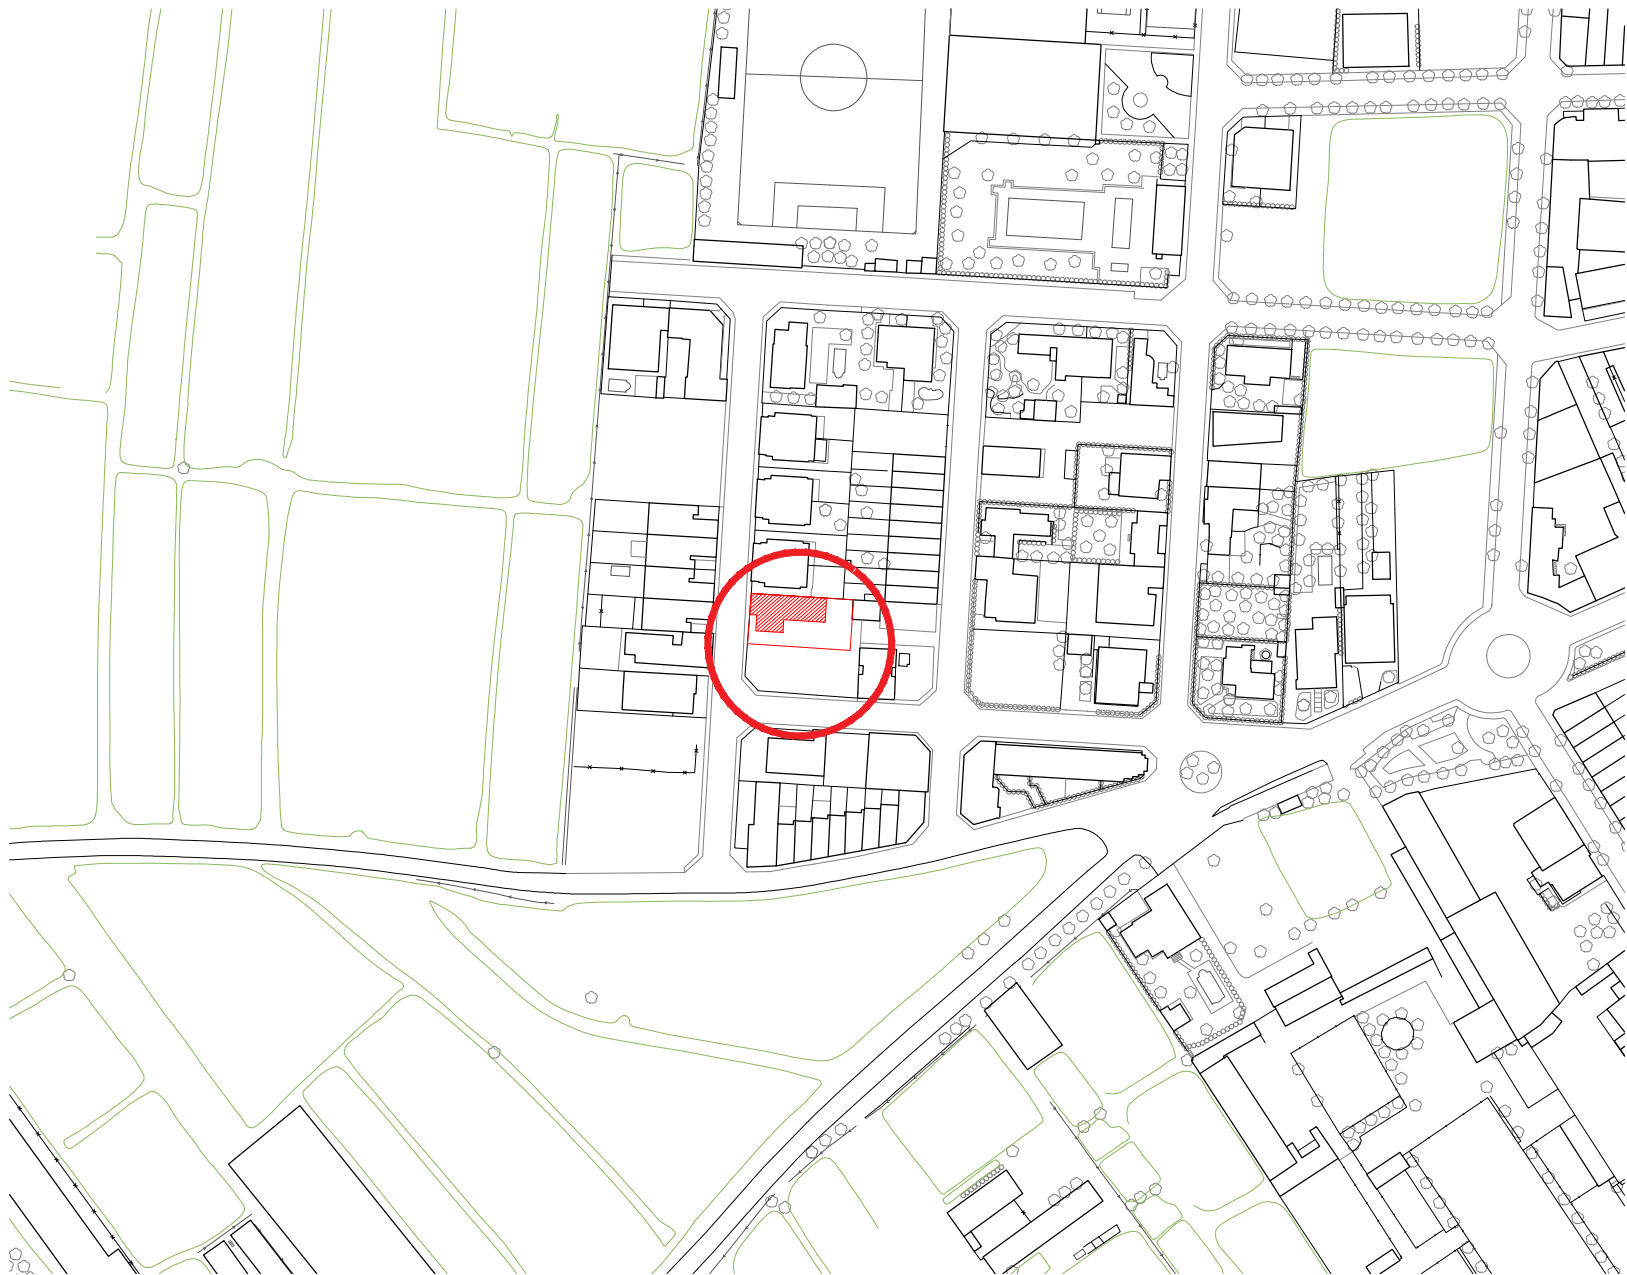



EMPLAÇAMENT e 1/2.500

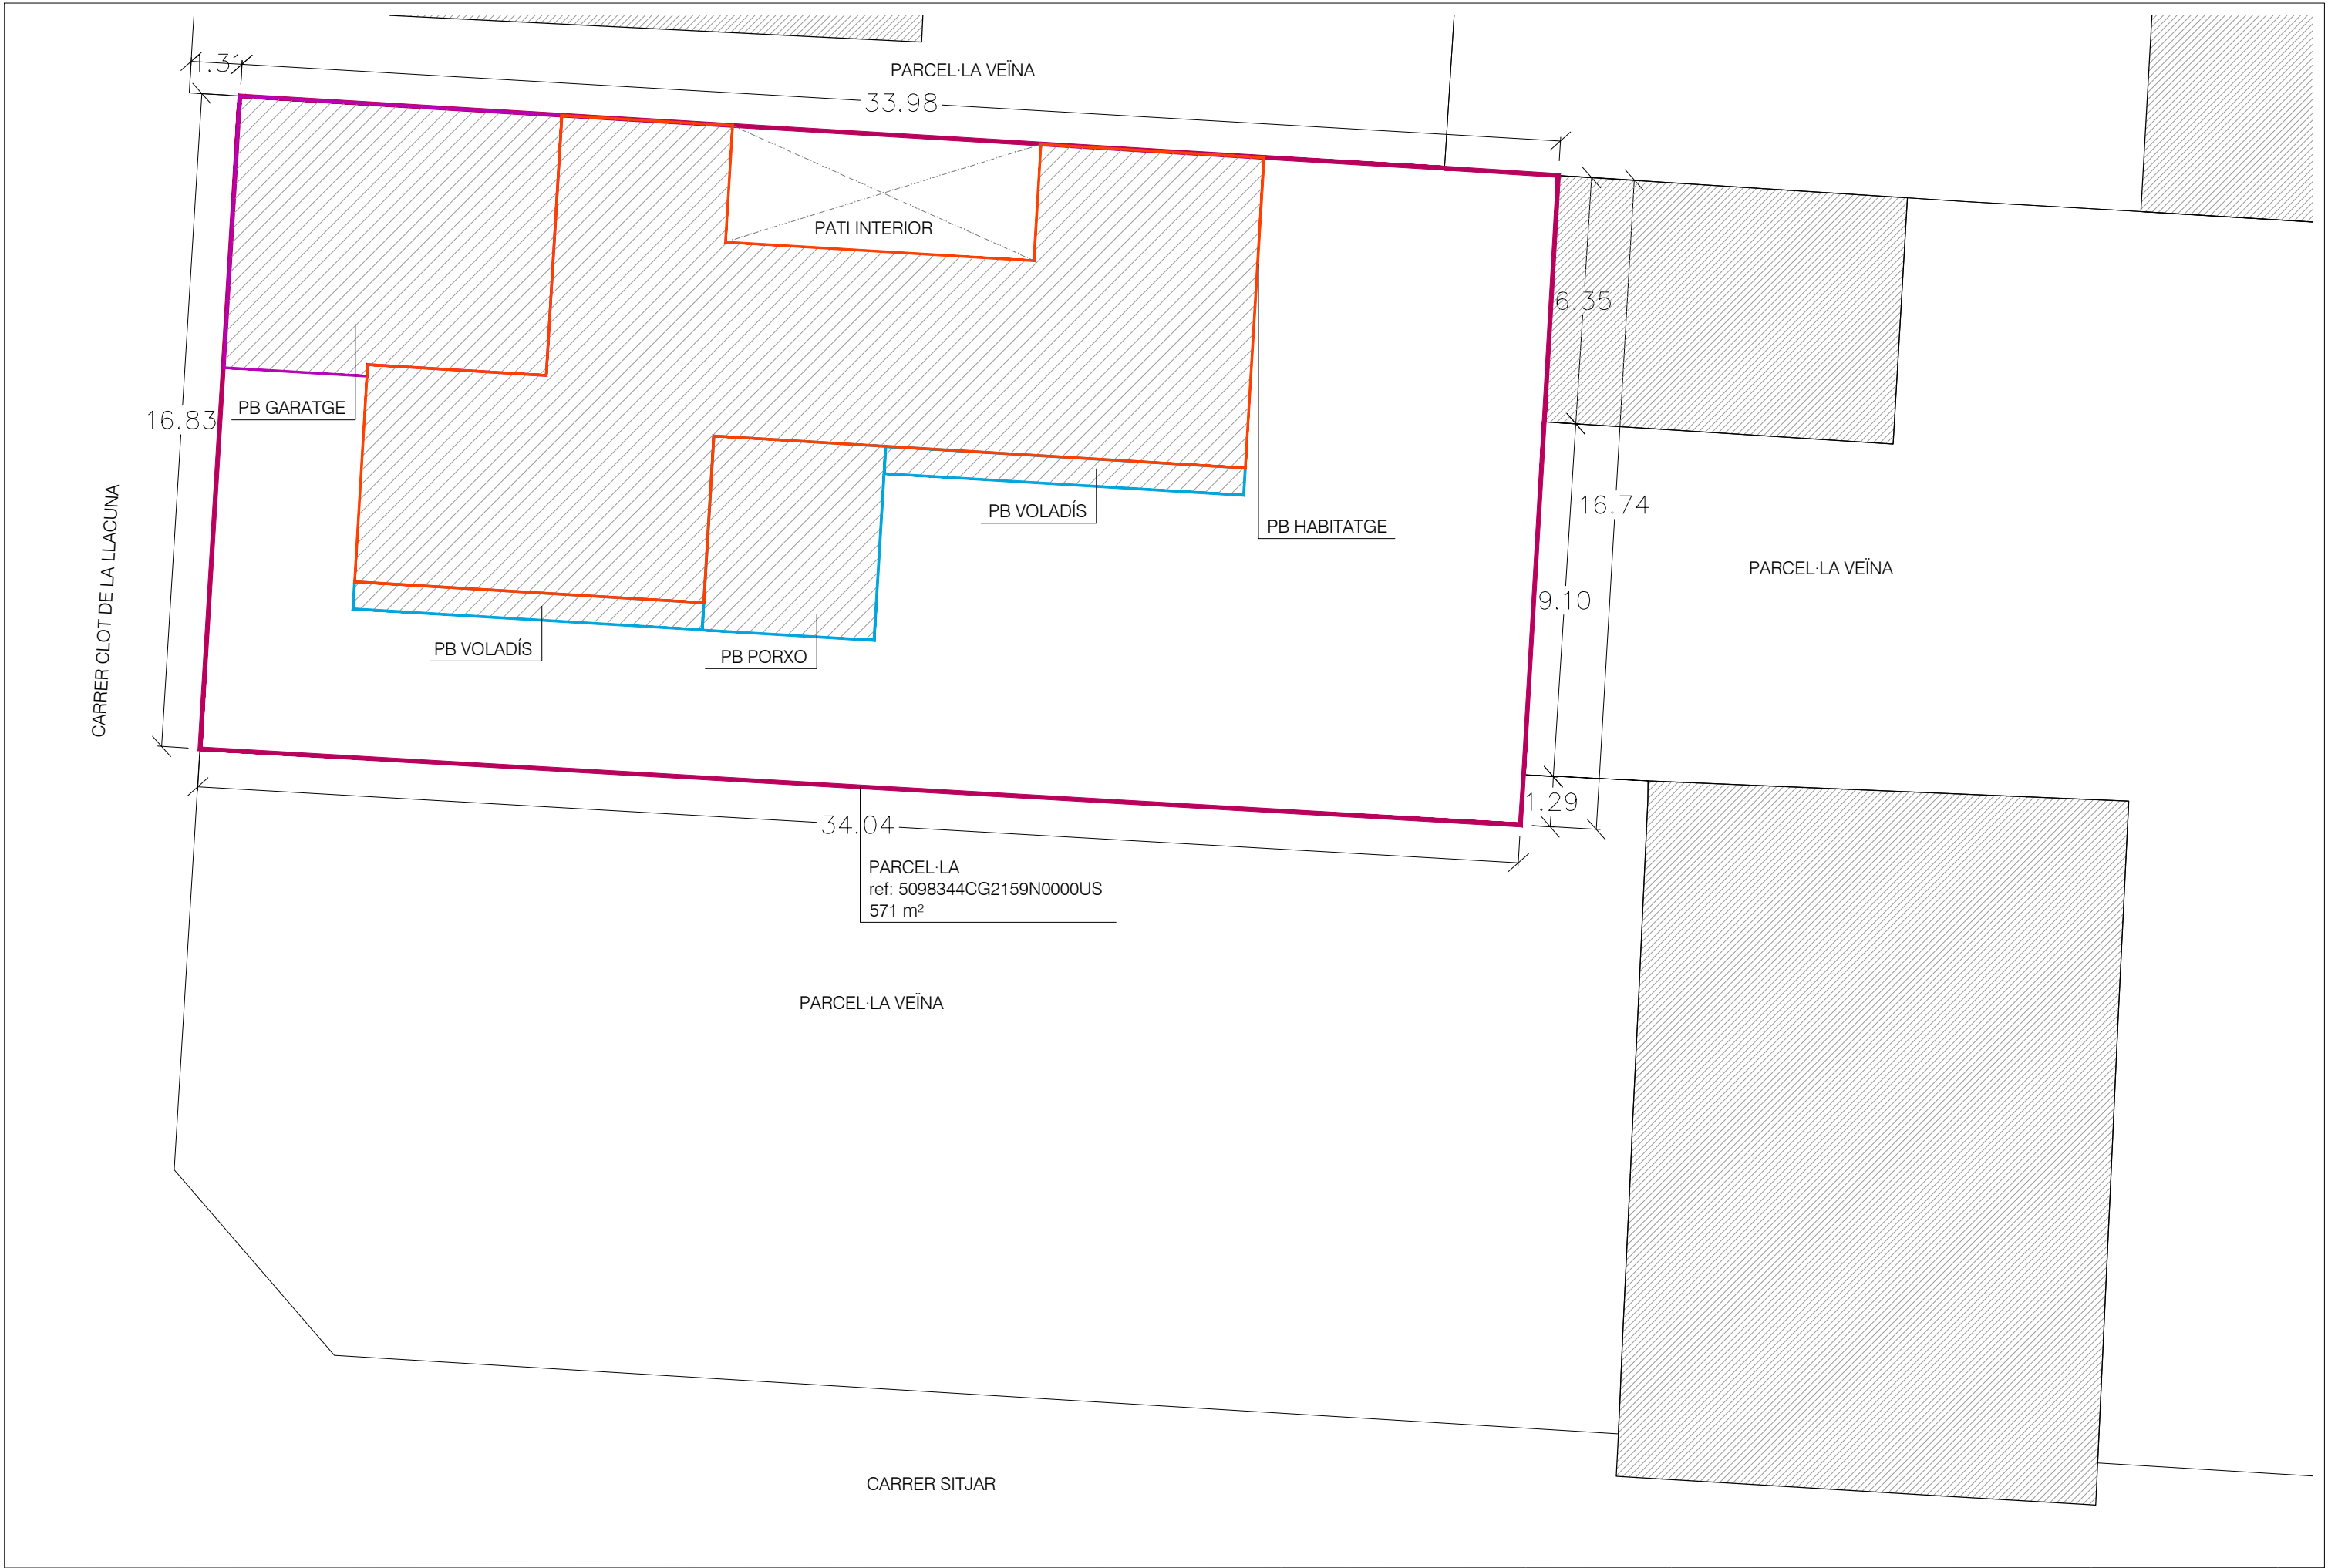

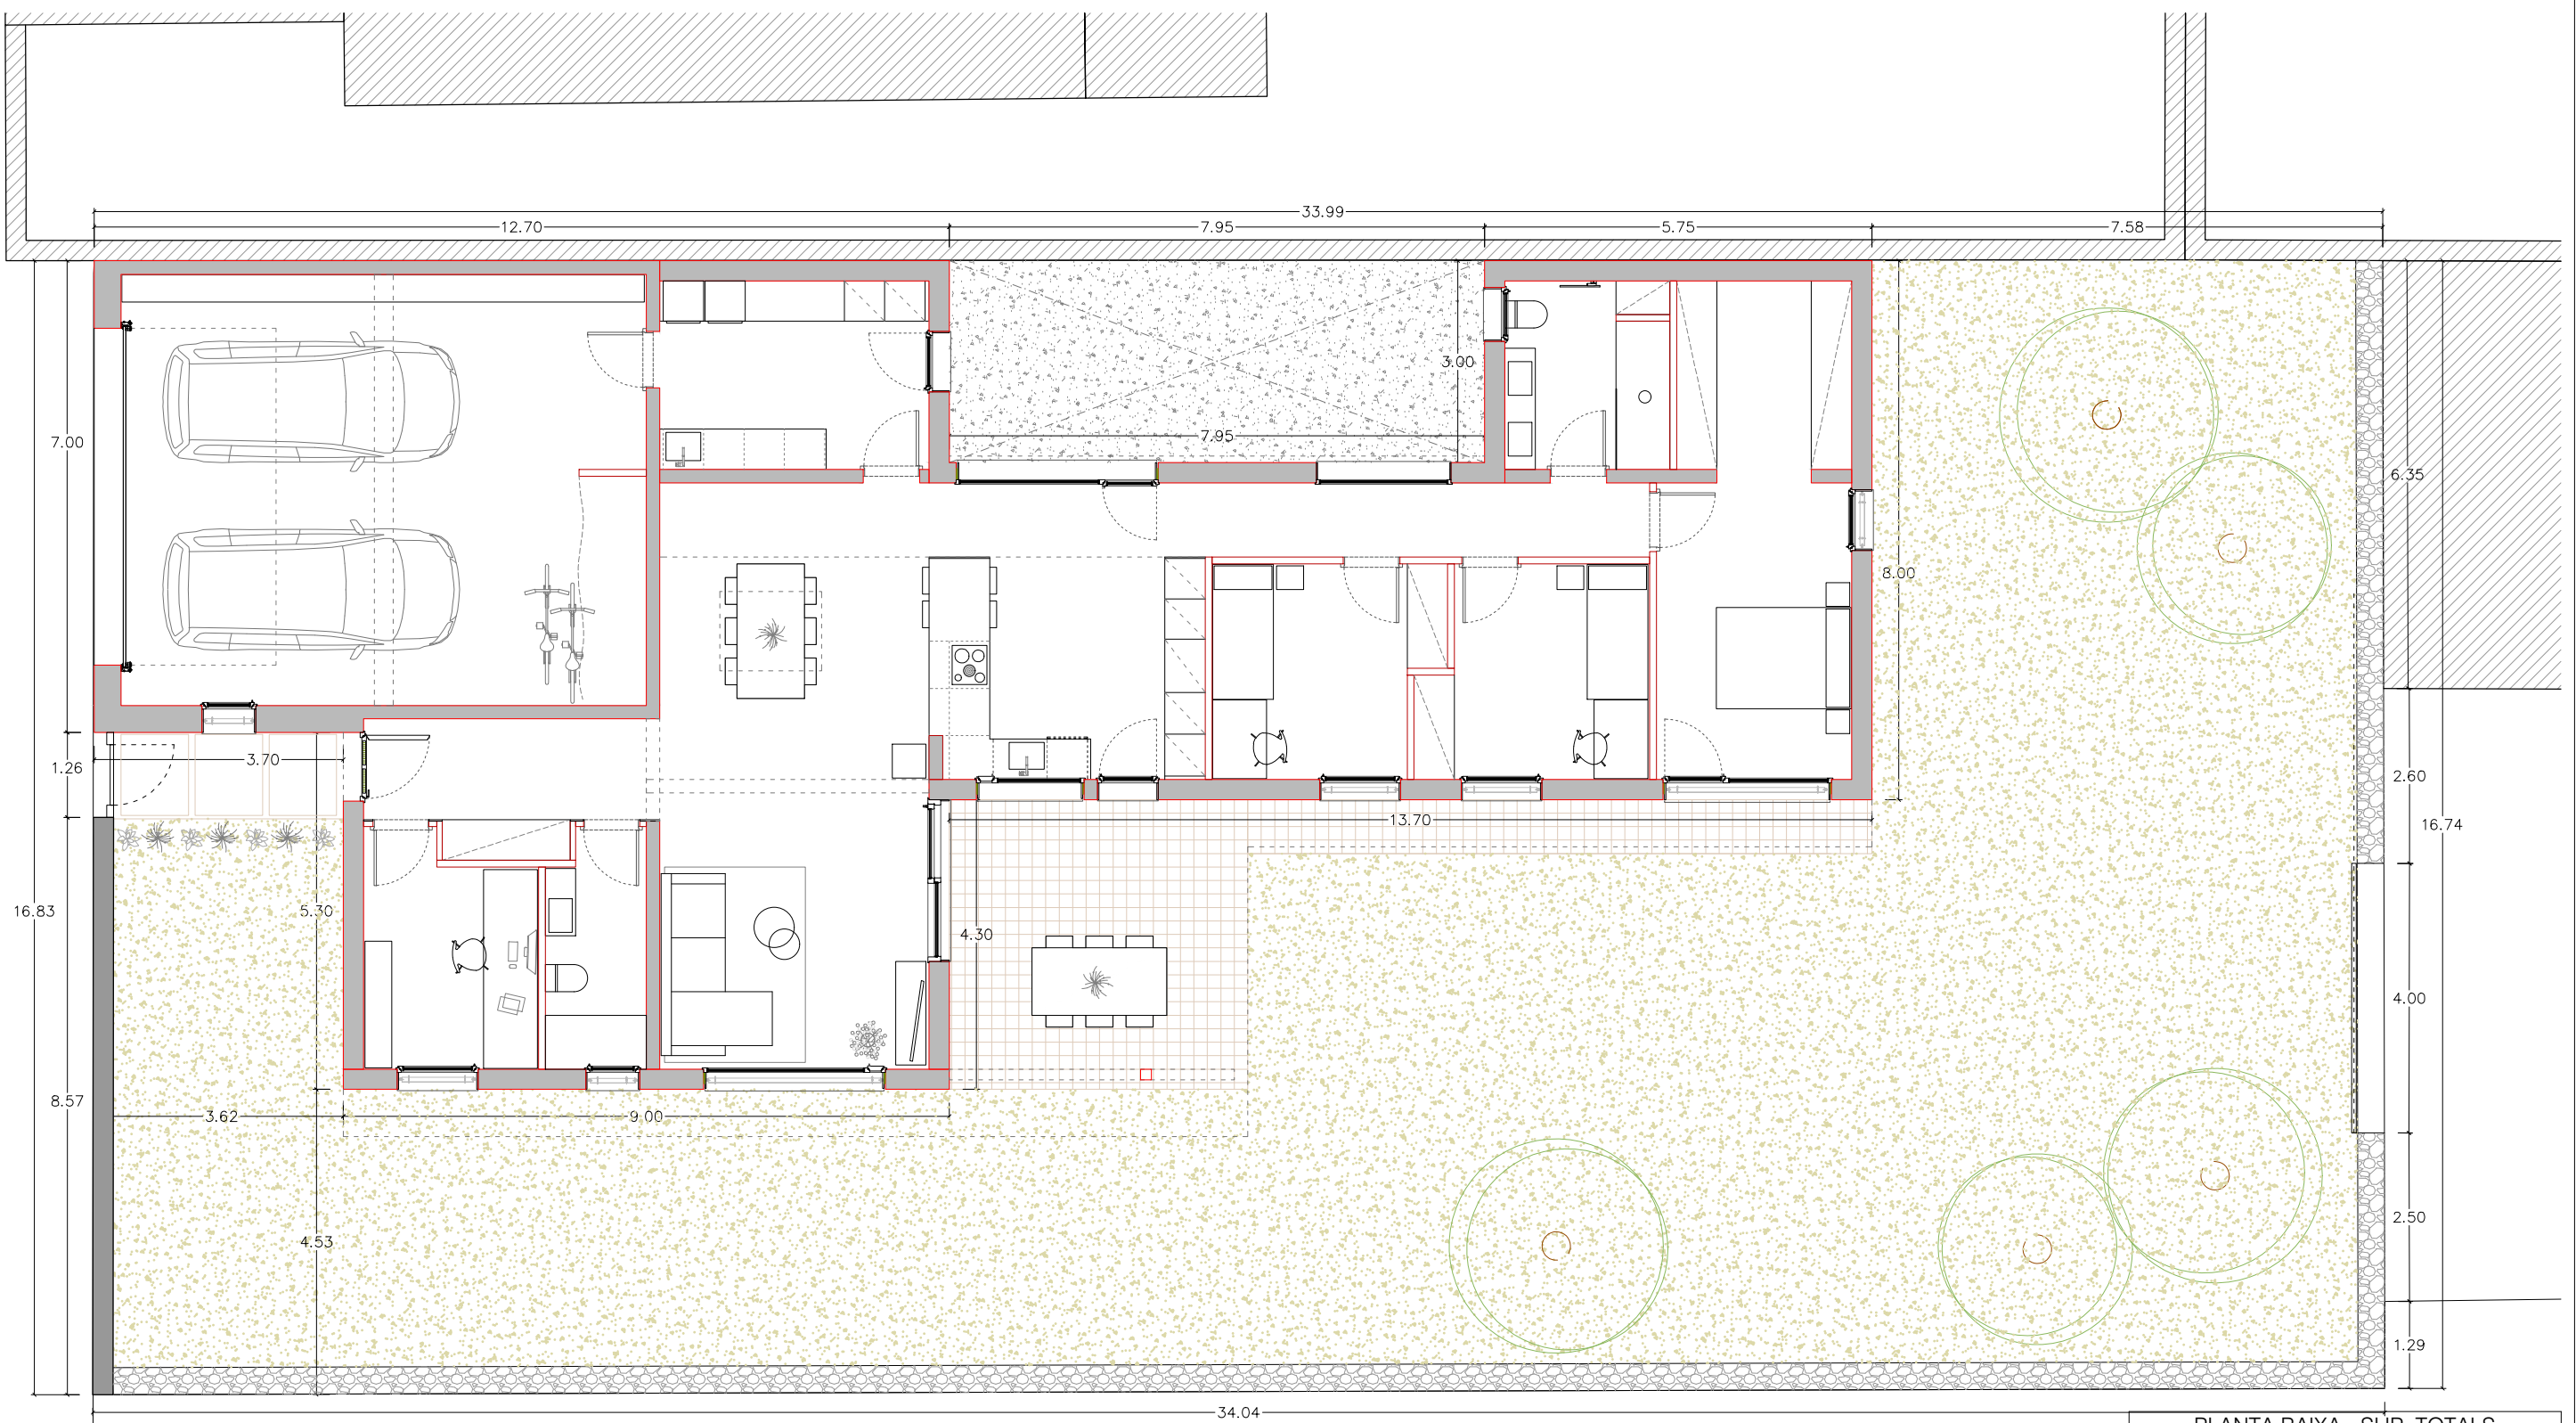

PLANTA BAIXA - SUP. TOTALS EDIFICACIÓ	
SUPERFÍCIES ÚTILS	
TOTAL EXTERIOR	306.46 m²
TOTAL NO HABITABLE	68.88 m²
TOTAL HABITATGE	140.27 m²
Superfície útil TOTAL Planta Baixa:	515.62 m²
SUPERFÍCIES CONSTRUÏDES	
TOTAL NO HABITABLE	28.55 m²
TOTAL NO HABITABLE	56.75 m²
TOTAL HABITATGE	165.61 m²
Superfície construïda TOTAL PBaixa:	250.91 m²

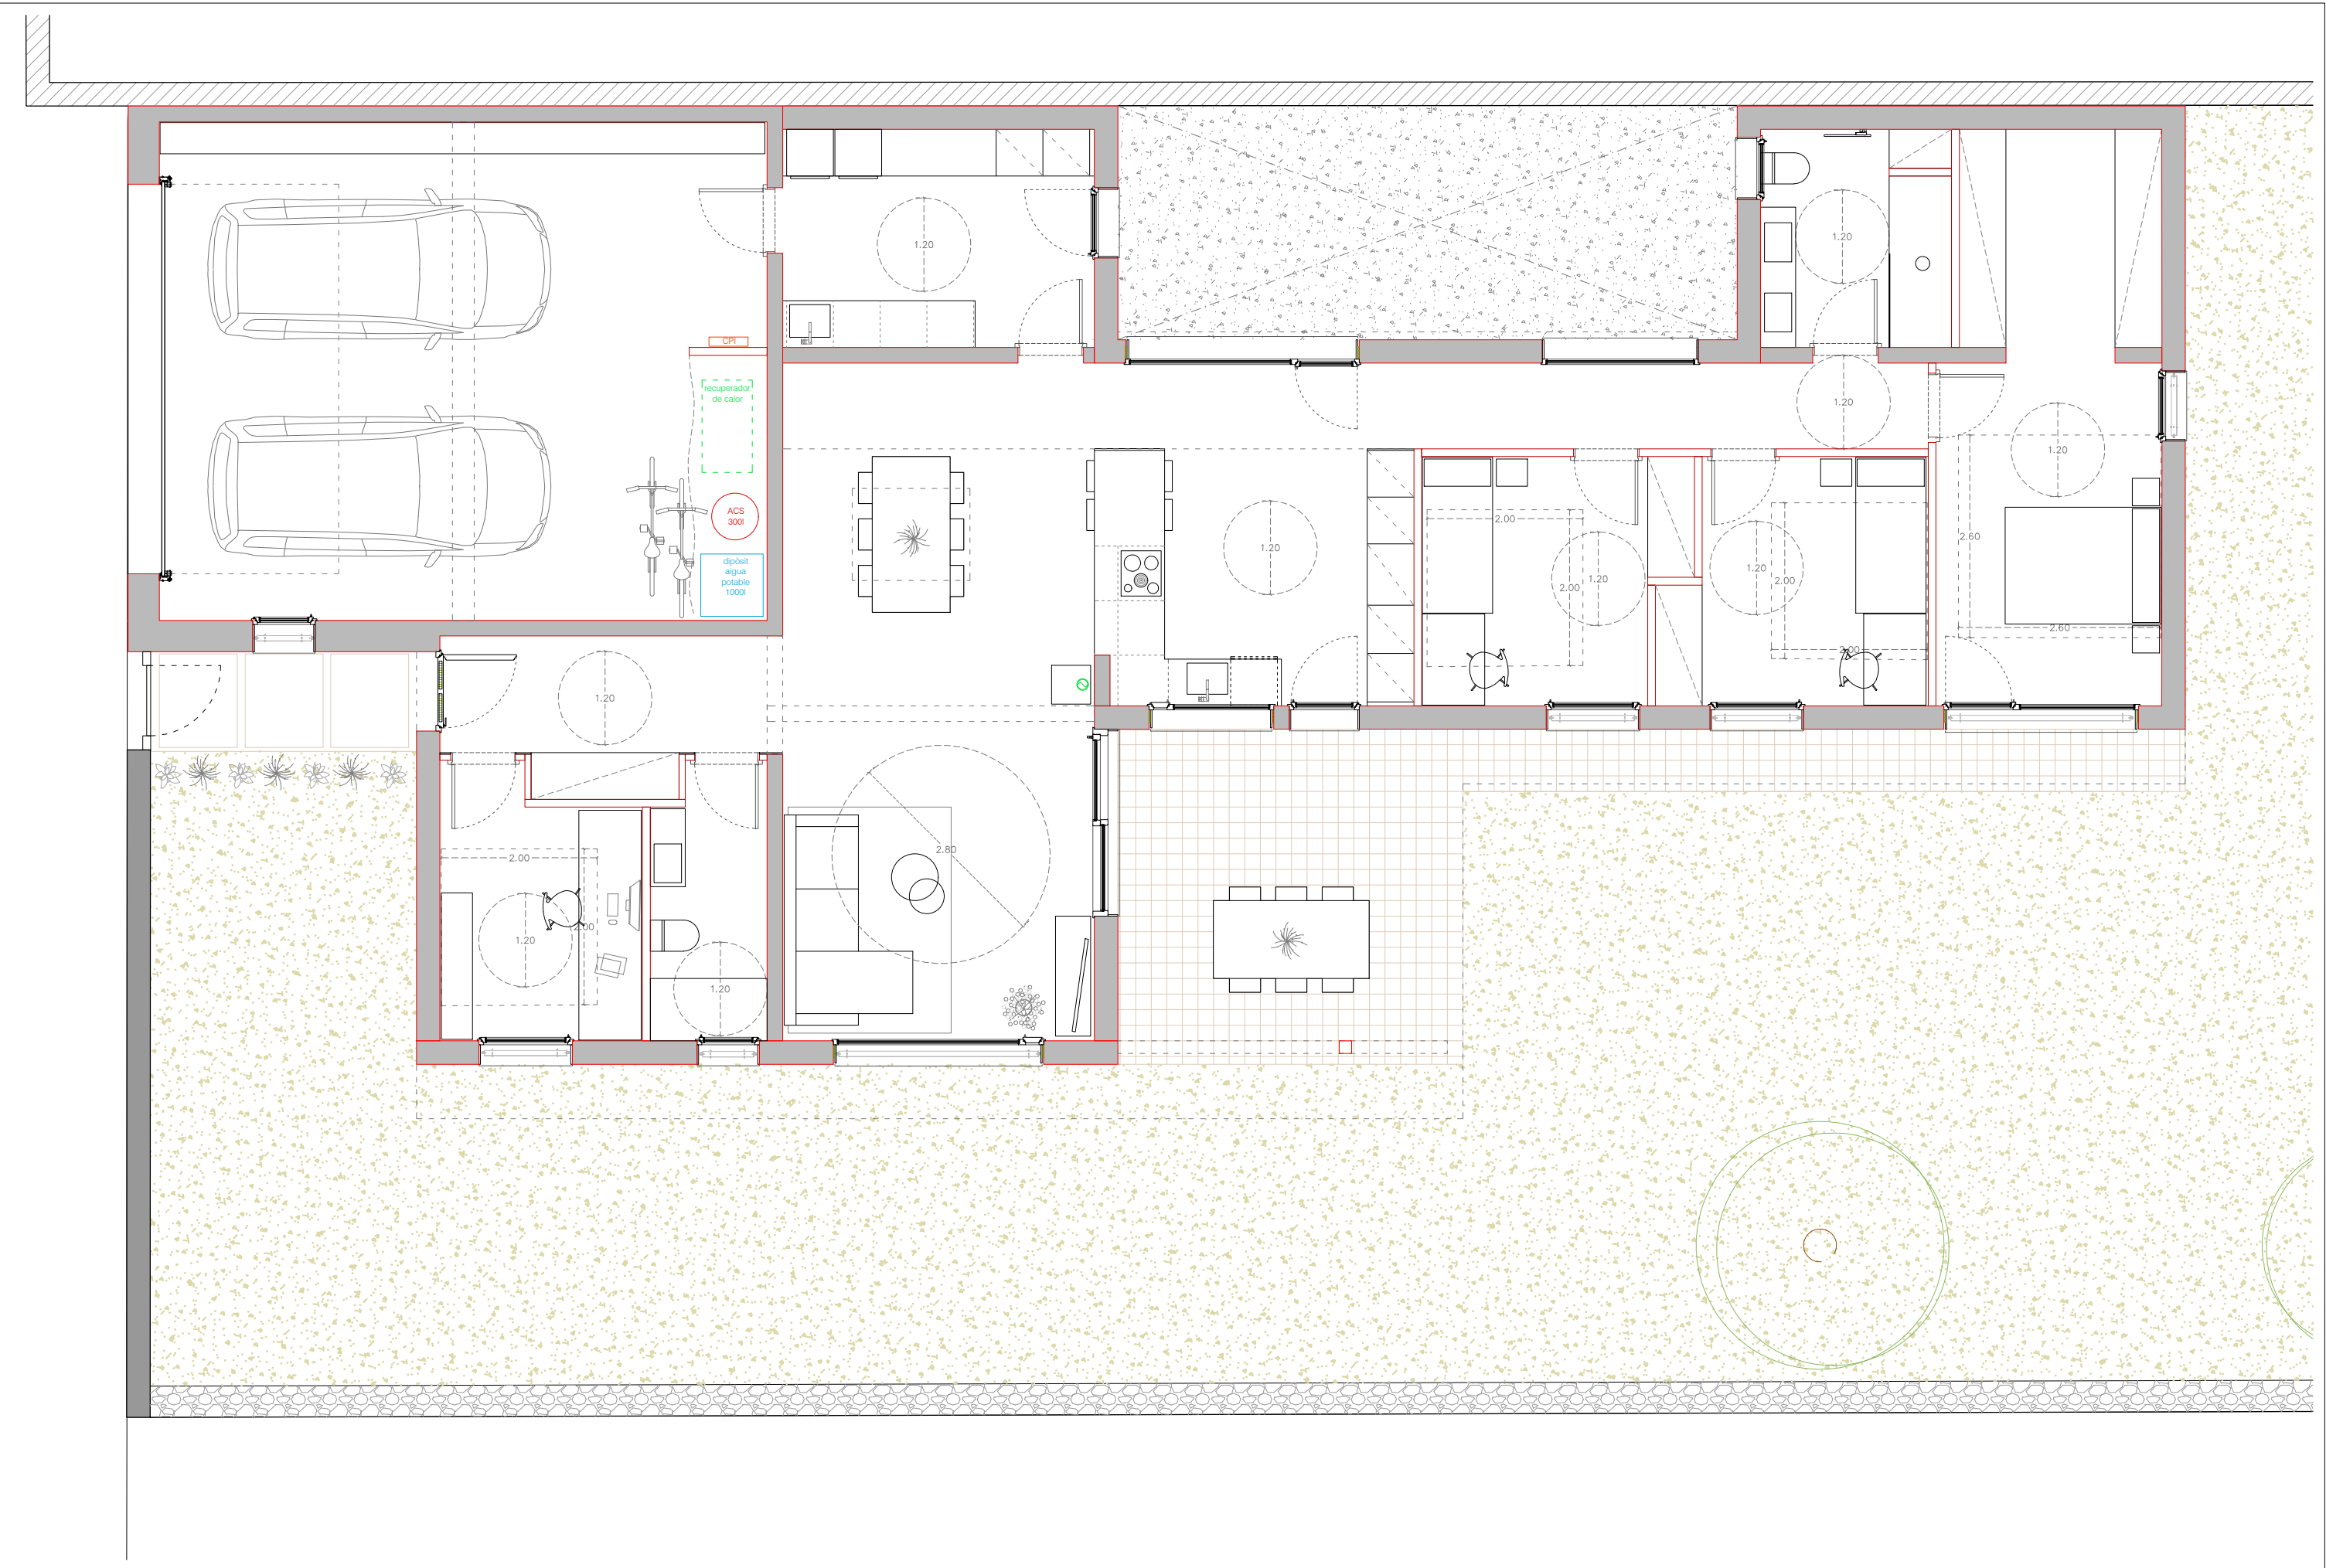

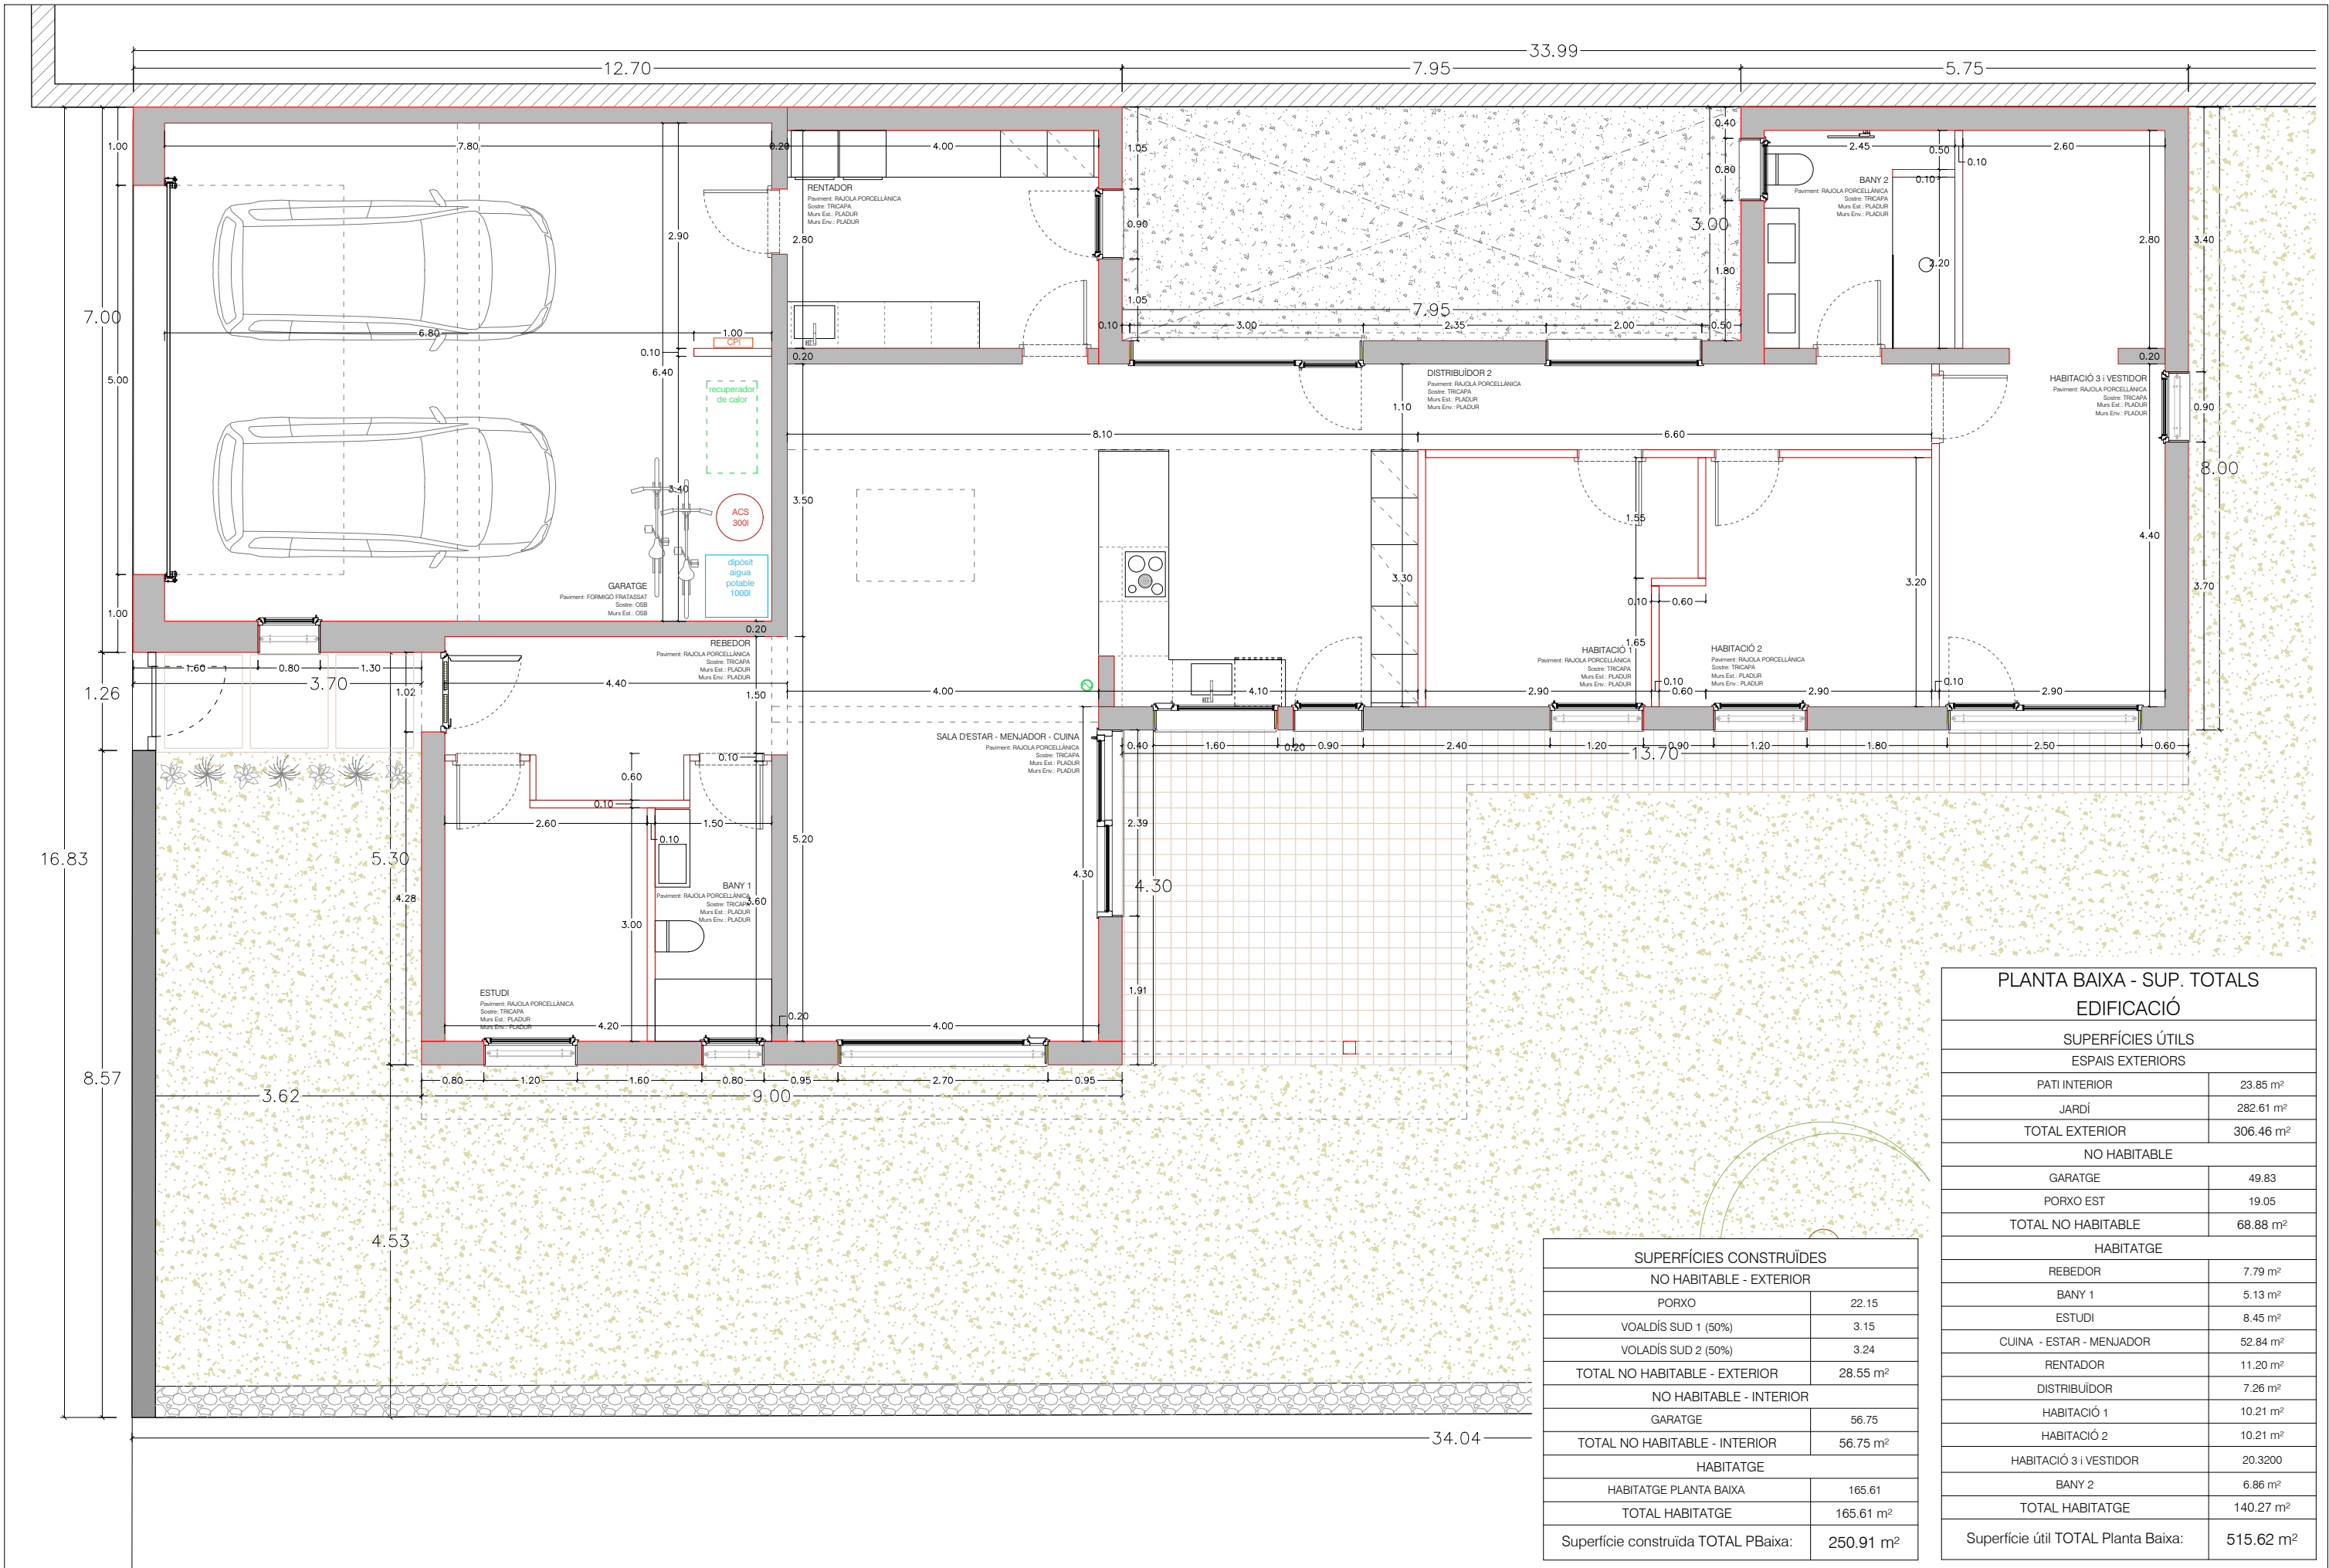

PLANTA BAIXA - SUP. TOTALS EDIFICACIÓ	
SUPERFÍCIES ÚTILS	
ESPAIS EXTERIORS	
PATÍ INTERIOR	23.85 m²
JARDÍ	282.61 m²
TOTAL EXTERIOR	306.46 m²
NO HABITABLE	
GARATGE	49.83
PORXO EST	19.05
TOTAL NO HABITABLE	68.88 m²
HABITATGE	
REBEDOR	7.79 m²
BANY 1	5.13 m²
ESTUDI	8.45 m²
CUINA - ESTAR - MENJADOR	52.84 m²
RENTADOR	11.20 m²
DISTRIBUIDOR	7.26 m²
HABITACIÓ 1	10.21 m²
HABITACIÓ 2	10.21 m²
HABITACIÓ 3 i VESTIDOR	20.3200
BANY 2	6.86 m²
TOTAL HABITATGE	140.27 m²
Superfície útil TOTAL Planta Baixa:	515.62 m²

SUPERFÍCIES CONSTRUÏDES	
NO HABITABLE - EXTERIOR	
PORXO	22.15
VOALDÍS SUD 1 (50%)	3.15
VOLADÍS SUD 2 (50%)	3.24
TOTAL NO HABITABLE - EXTERIOR	28.55 m²
NO HABITABLE - INTERIOR	
GARATGE	56.75
TOTAL NO HABITABLE - INTERIOR	56.75 m²
HABITATGE	
HABITATGE PLANTA BAIXA	165.61
TOTAL HABITATGE	165.61 m²
Superfície construïda TOTAL PBaixa:	250.91 m²

